

Liste des pièces constitutives du présent dossier	
PC 01.a	Plan de situation (carte IGN)
PC 01.b	Plan de situation (plan cadastral)
PC 01.c	Plan de situation (vue aérienne)
PC 02.a	Plan de masse SDIS
PC 02.b	Plan de masse état existant
PC 02.c	Plan de masse état projeté
PC 02.d	Plan de masse état projeté (zoom)
PC 03	Coupe de terrain
PC 04	Notice descriptive
PC 05.a	Plan de façades
PC 05.b	Plan de toiture
PC 06	Insertion paysagère
PC 07	Documents photographiques
PC 08	Documents photographiques
PC ANNEXE	Plan d'aménagement intérieur
PC ANNEXE	Coordonnées GPS

PERMIS DE CONSTRUIRE

Bâtiment à usage équestre avec toiture photovoltaïque

Maître d'ouvrage :
ECURIE DE MYRISSE
15 Chemin de Jeantoulic - 33770 SALLES

Adresse du projet :
La Grande Pièce
33770 SALLES

- Section 000 F 3693
Superficie 23 418m²

- Section 000 F 3697
Superficie 12 327m²





UN ARCHIT DANS LES BOIS

Tresseras Architecture - Siret 882 278 120 00010
Lieu dit " Le Billon " - 33840 CAPTIEUX
07 57 87 99 10 - mathieu@unarchidanslesbo.is



PROJET

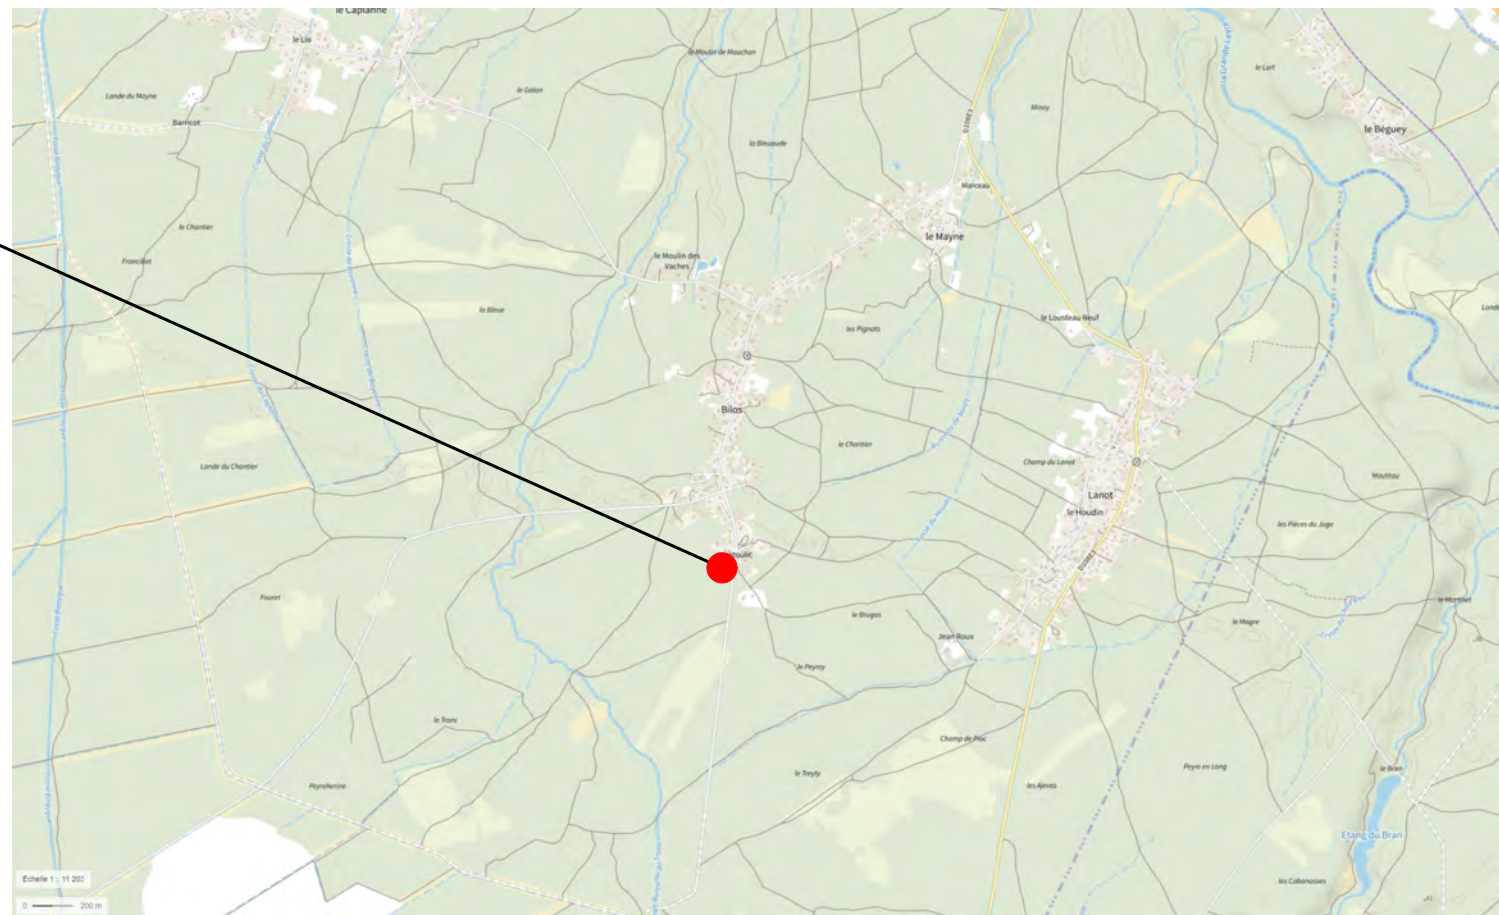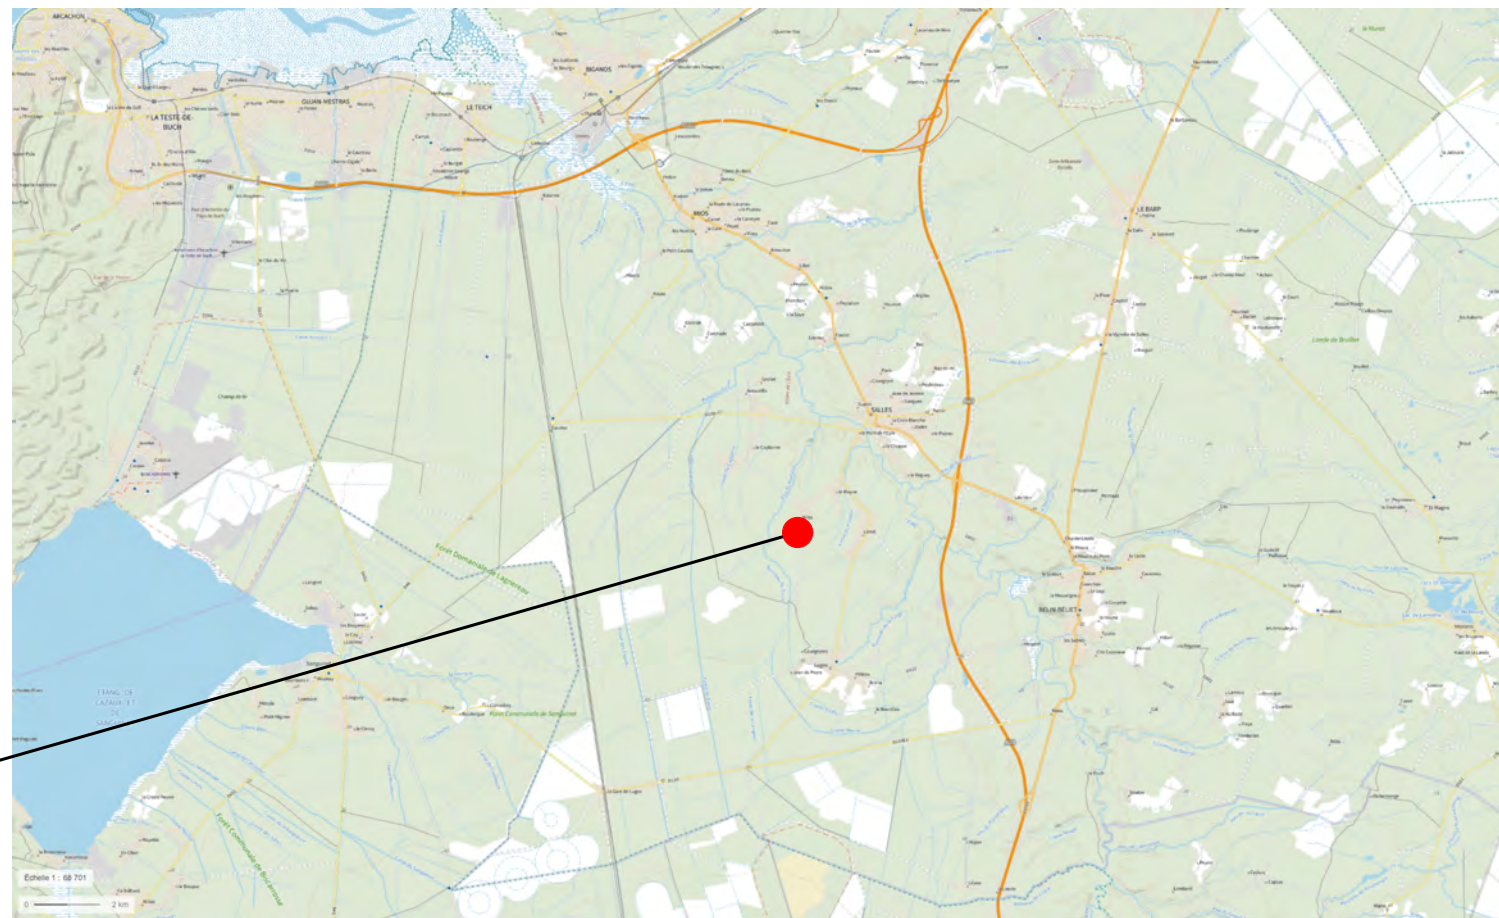

Tresseras Architecture
882 278 120 00010
06 80 70 39 93
Le Billon - 33840 Captieux

Tresseras Architecture - Siret 882 278 120 00010
Lieu dit " Le Billon " - 33840 CAPTIEUX
07 57 87 99 10 - mathieu@unarchidanslesbois



Bâtiment à usage équestre avec toiture photovoltaïque

La Grande Pièce - 33770 SALLES

ECURIE DE MYRISSE

15 Chemin de Jeantouluc - 33770 SALLES


Plan de situation (carte IGN)

Echelle :

Date : 09/04/2024

PC
01.a

Les présents plans sont exclusivement destinés à l'obtention de l'autorisation administrative. Ils ne sont pas des plans d'exécution et ne peuvent en aucun cas servir à la réalisation de la construction.

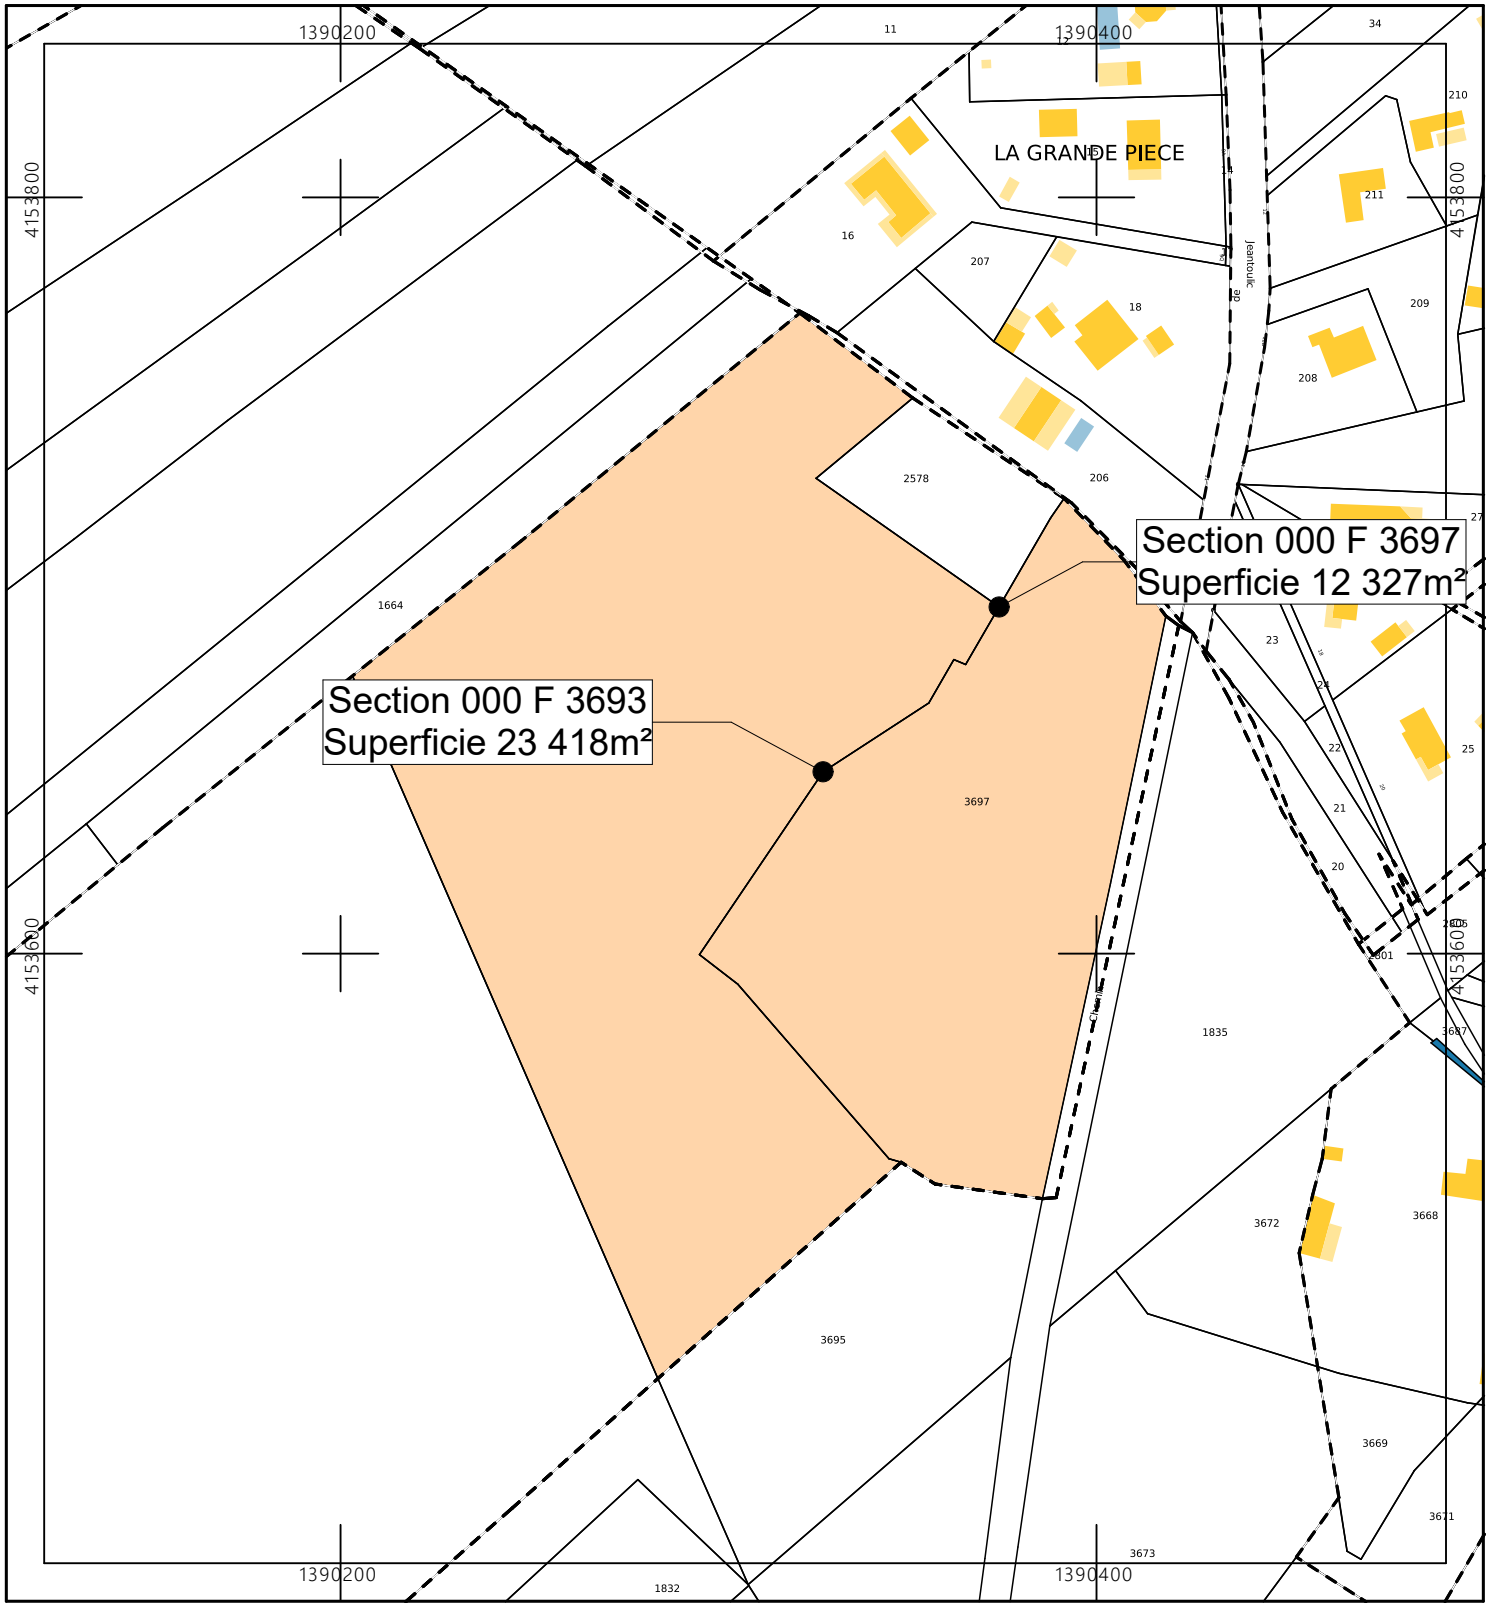

Parcelles cadastrales

- Section 000 F 3693
Superficie 23 418m²
- Section 000 F 3697
Superficie 12 327m²

Superficie Total 35 745m²

Tresseras Architecture
882 278 120 00010
06 80 70 39 93
Le Billon - 33840 Captieux

Tresseras Architecture - Siret 882 278 120 00010
Lieu dit " Le Billon " - 33840 CAPTIEUX
07 57 87 99 10 - mathieu@unarchidanslesbois



Bâtiment à usage équestre avec toiture photovoltaïque

La Grande Pièce - 33770 SALLES

ECURIE DE MYRISSE


15 Chemin de Jeantouluc - 33770 SALLES

Plan de situation (plan cadastral)

Echelle : 1:2000

Date : 09/04/2024

PC
01.b

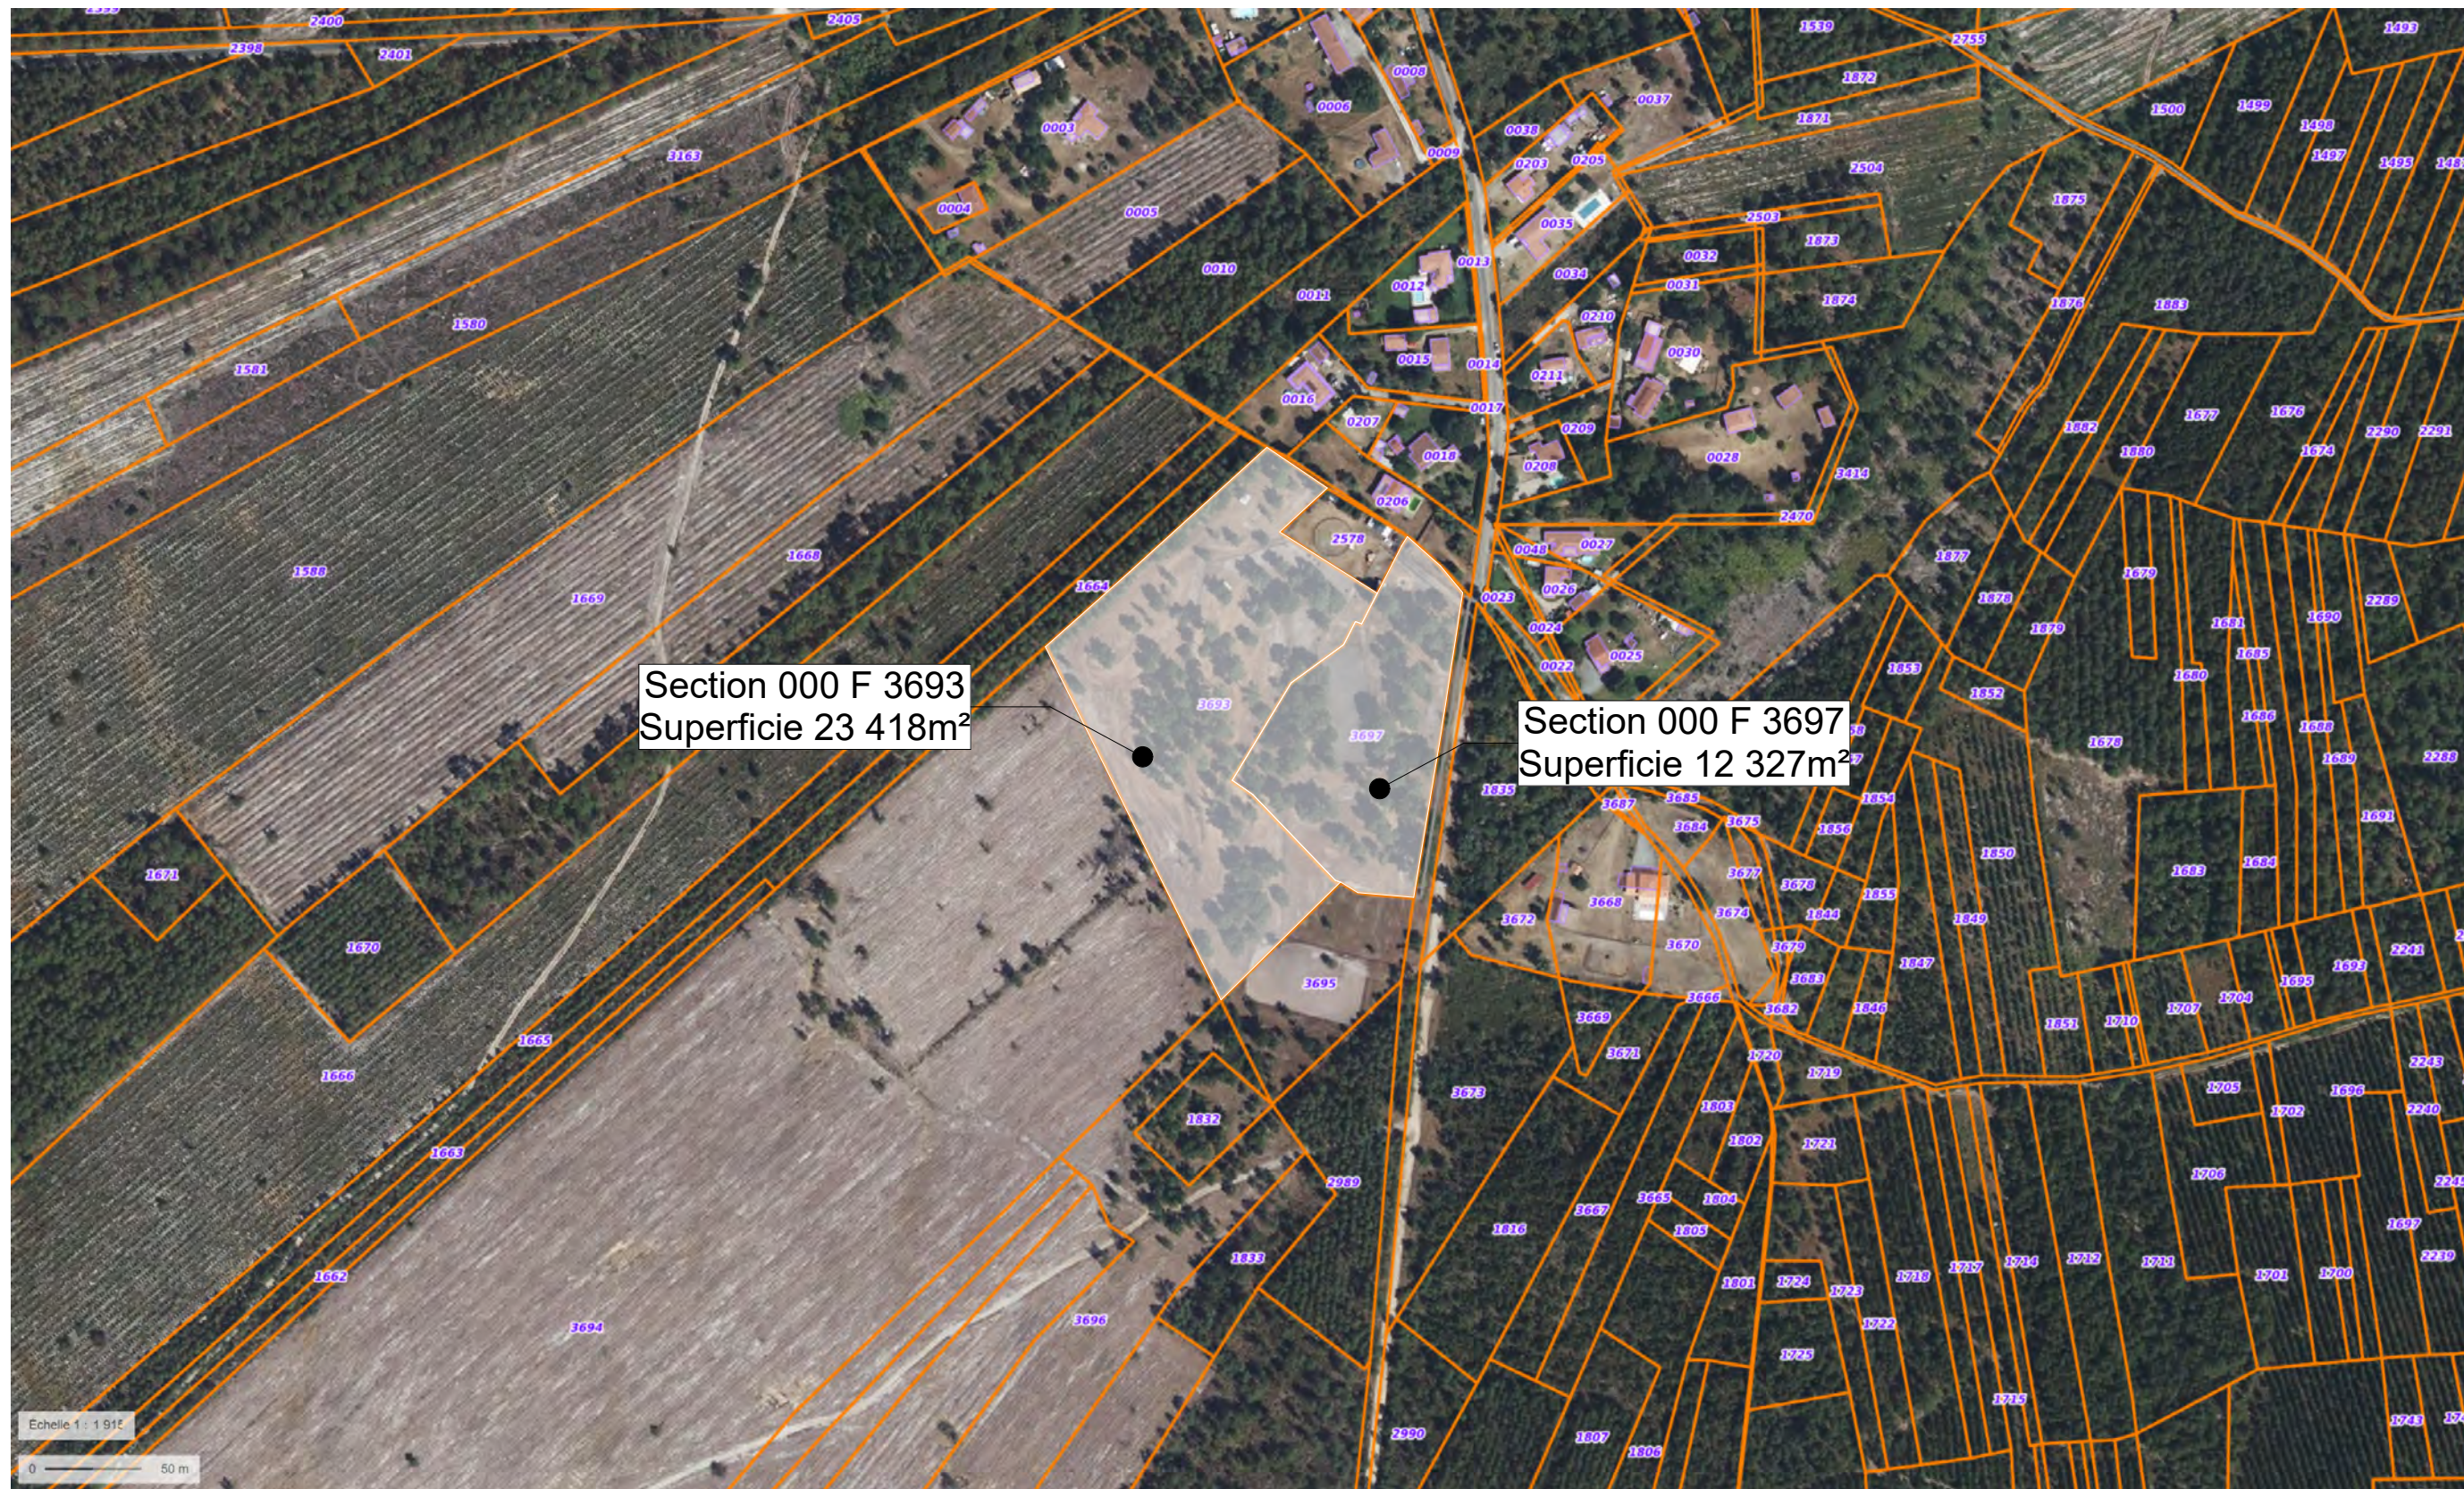

Tresseras Architecture
882 278 120 00010
06 80 70 39 93
Le Billon - 33840 Captieux


Tresseras Architecture - Siret 882 278 120 00010
Lieu dit " Le Billon " - 33840 CAPTIEUX
07 57 87 99 10 - mathieu@unarchidanslesbois




Bâtiment à usage équestre avec toiture photovoltaïque
La Grande Pièce - 33770 SALLES
ECURIE DE MYRISSE
15 Chemin de Jeantouluc - 33770 SALLES

Plan de situation (vue aérienne)
Echelle :
Date : 09/04/2024

PC
01.c

 

02.a

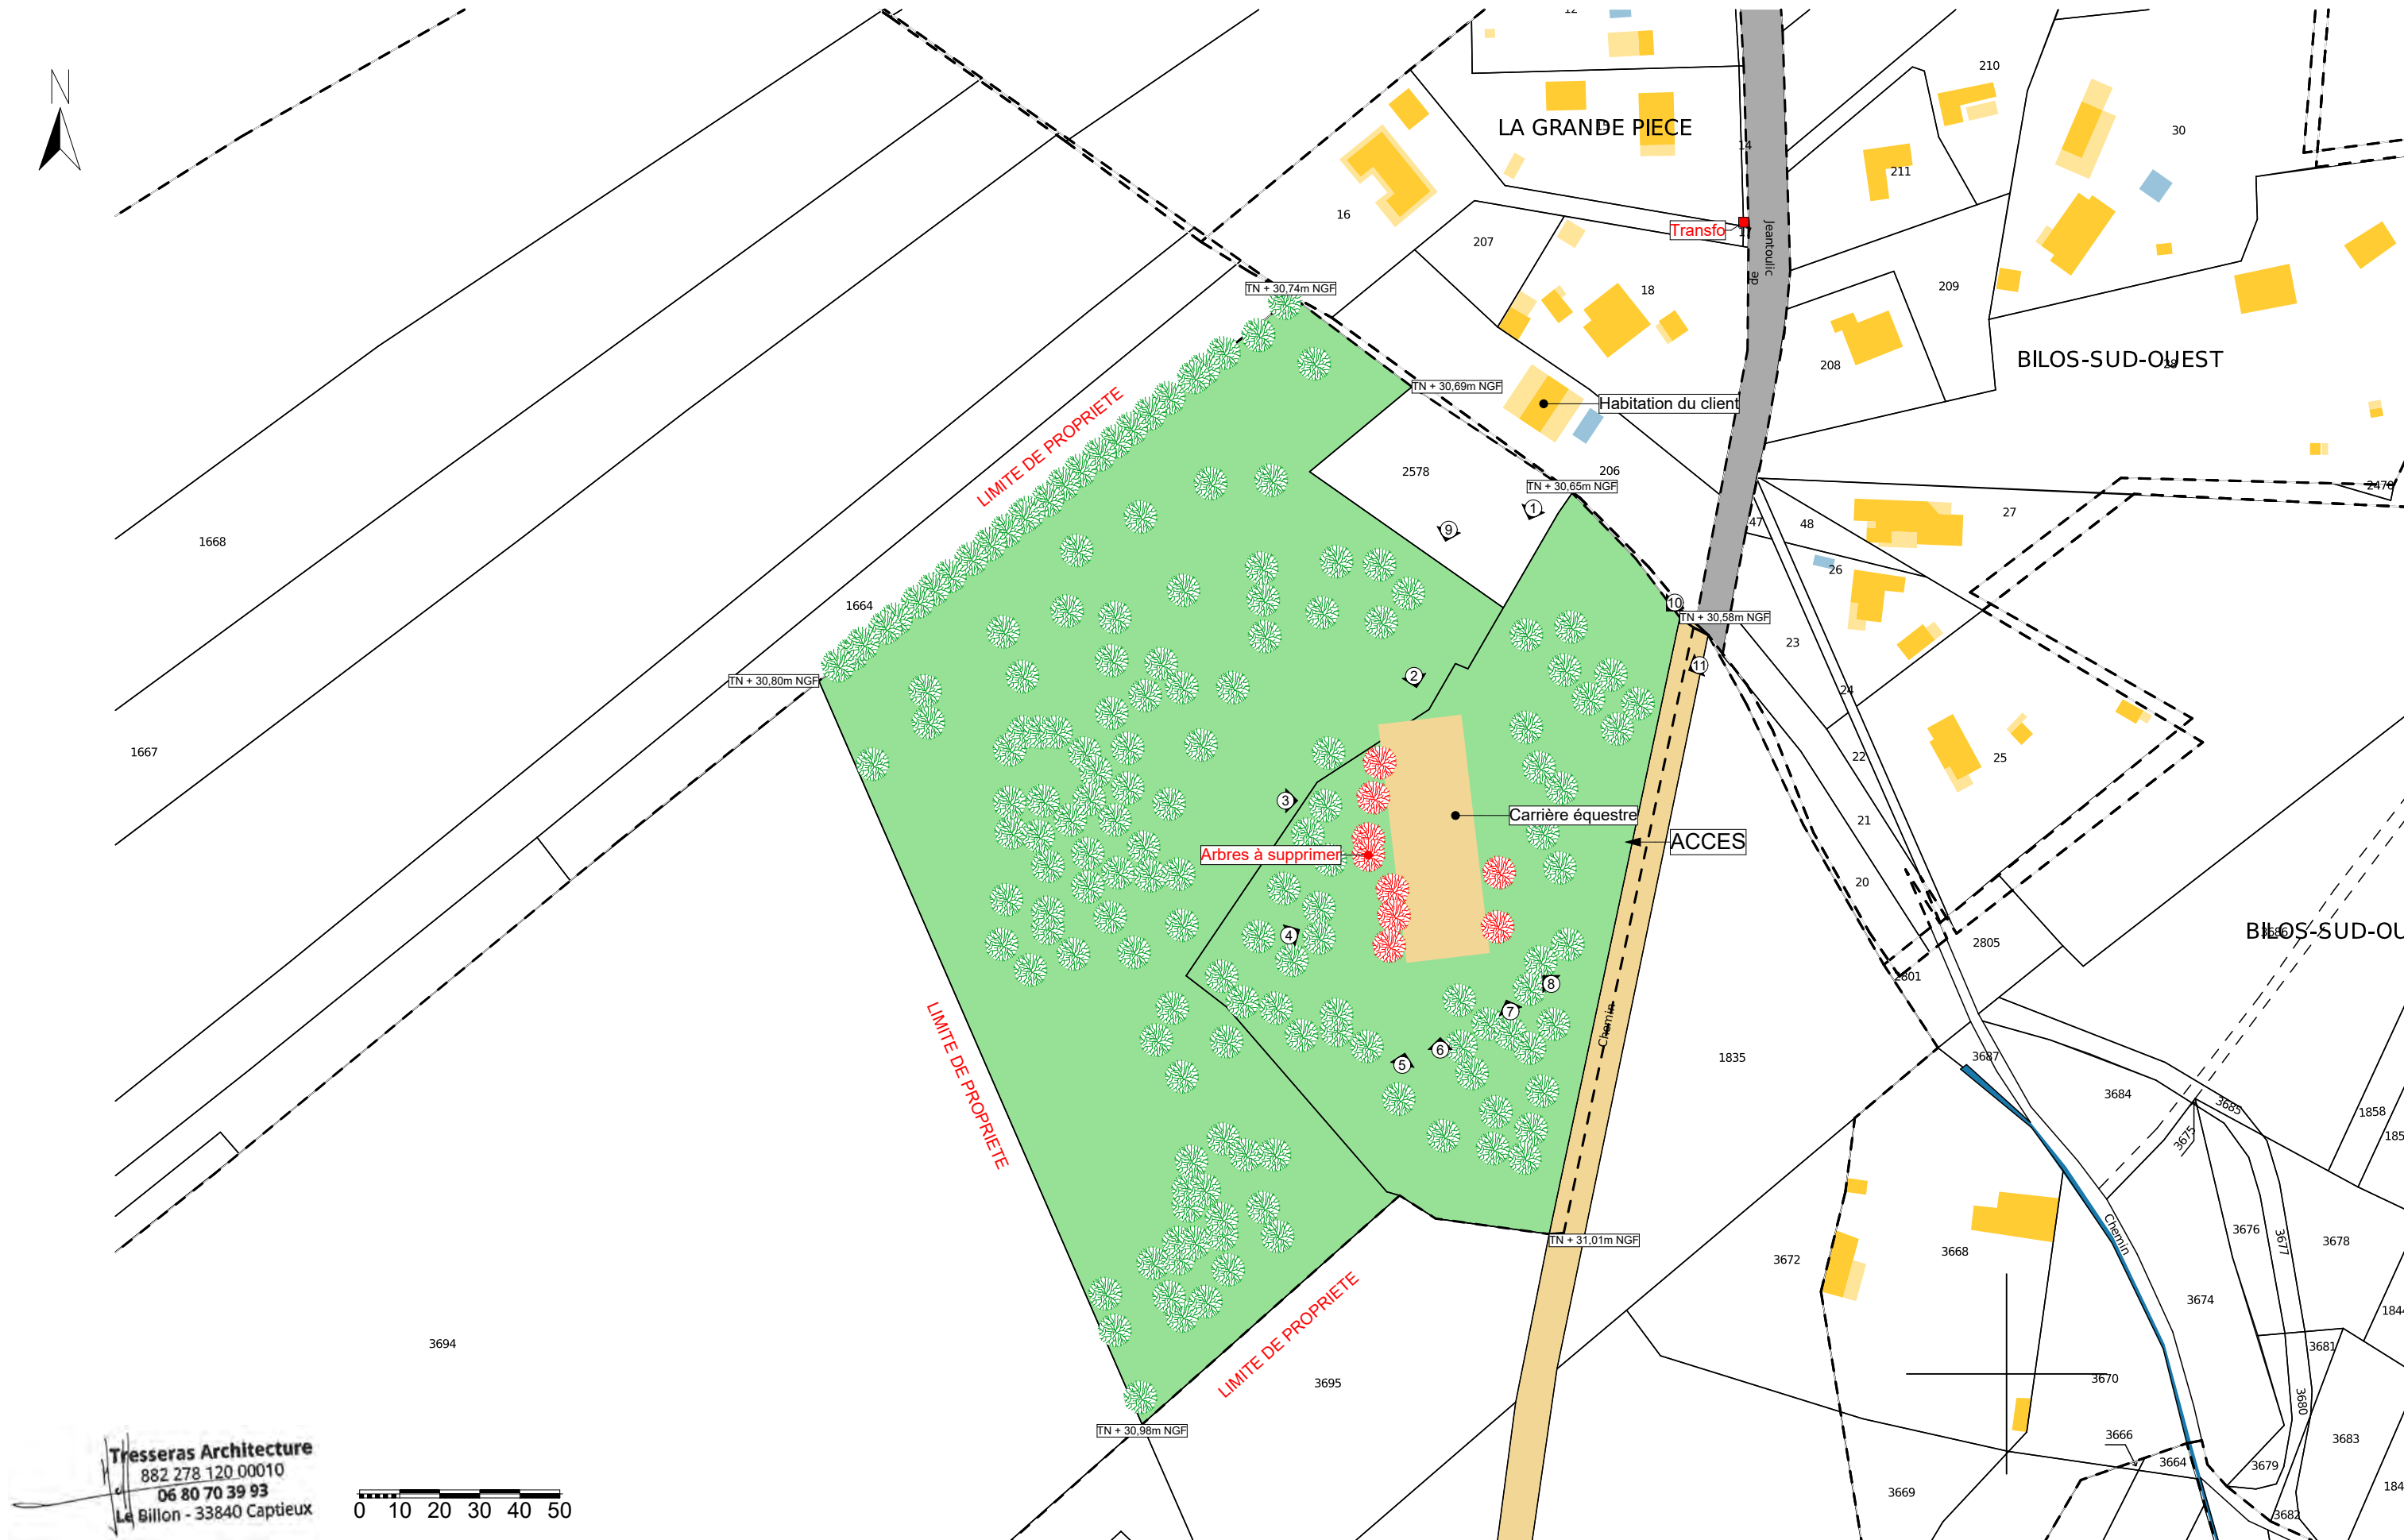

Tresseras Architecture
882 278 120 00010
06 80 70 39 93
Le Billon - 33840 Captieux

0 10 20 30 40 50

Tresseras Architecture - Siret 882 278 120 00010
Lieu dit " Le Billon " - 33840 CAPTIEUX
07 57 87 99 10 - mathieu@unarchidanslesbois



Bâtiment à usage équestre avec toiture photovoltaïque

La Grande Pièce - 33770 SALLES

ECURIE DE MYRISSE

15 Chemin de Jeantouluc - 33770 SALLES


Plan de masse état existant

Echelle : 1:1500

Date : 09/04/2024

PC

02.b

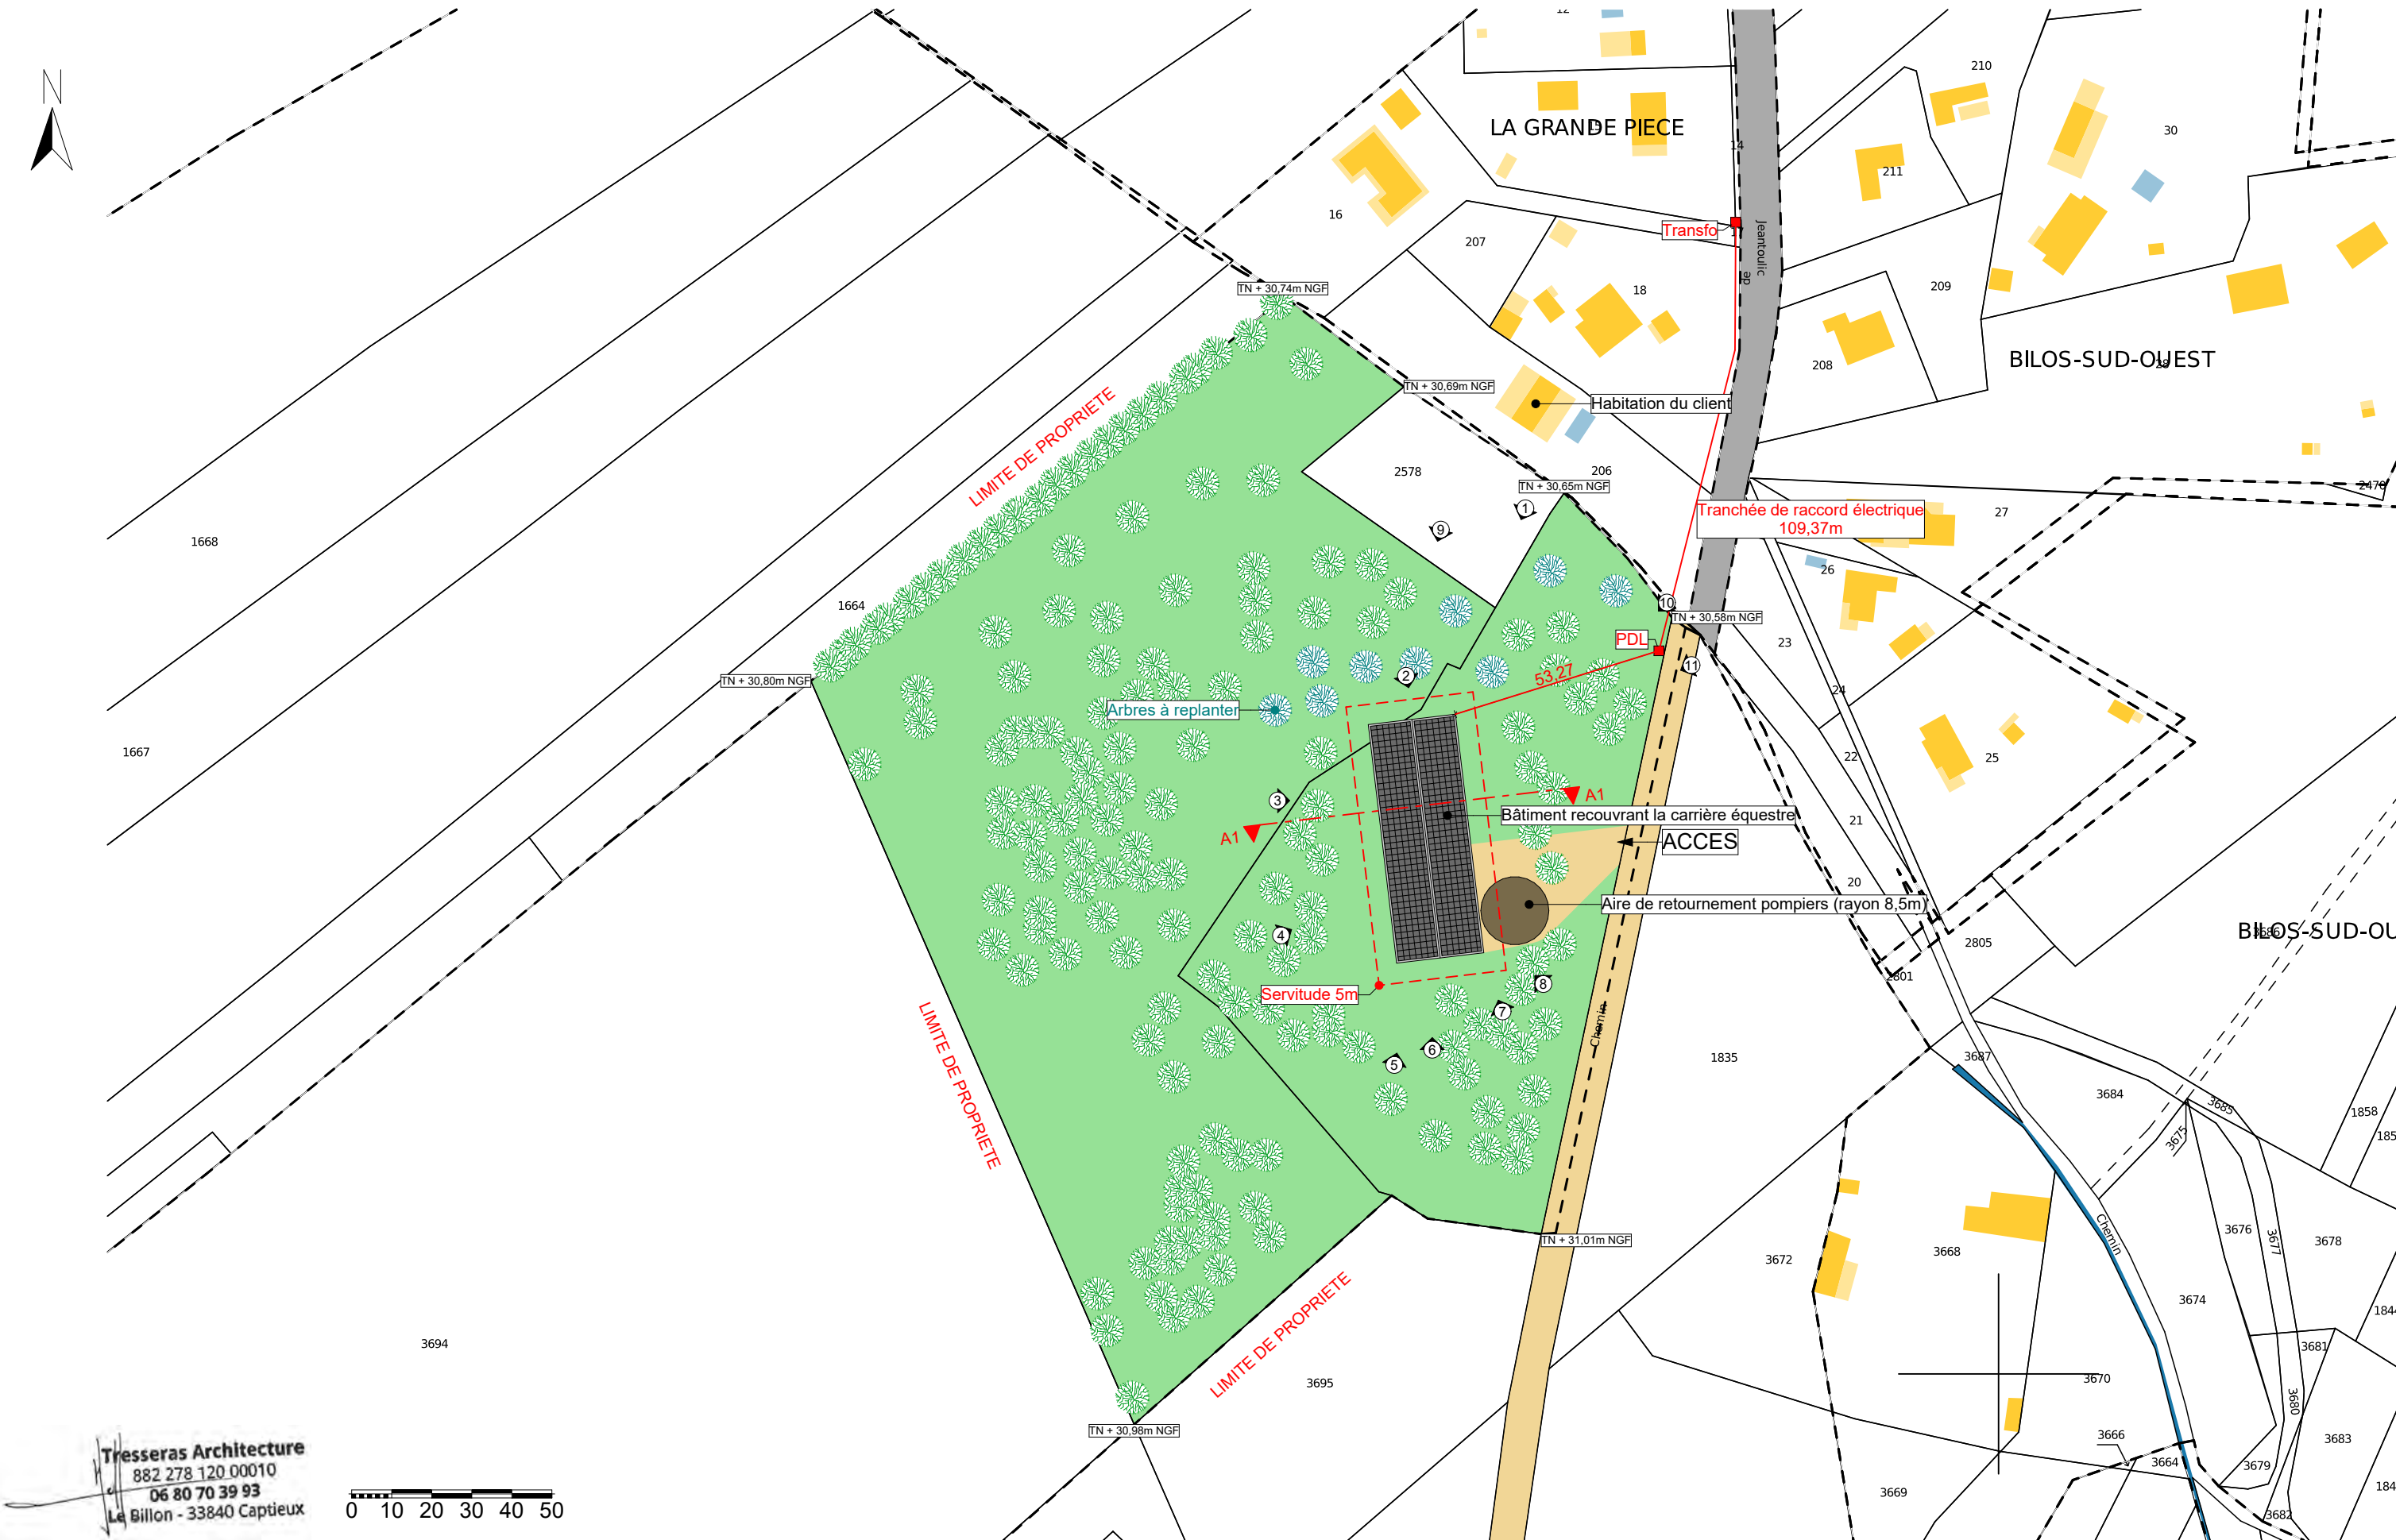

Tresseras Architecture
882 278 120 00010
06 80 70 39 93
Le Billon - 33840 Captieux

0 10 20 30 40 50

Tresseras Architecture - Siret 882 278 120 00010
Lieu dit " Le Billon " - 33840 CAPTIEUX
07 57 87 99 10 - mathieu@unarchidanslesbois



Bâtiment à usage équestre avec toiture photovoltaïque

La Grande Pièce - 33770 SALLES

ECURIE DE MYRISSE

15 Chemin de Jeantouluc - 33770 SALLES


Plan de masse état projeté

Echelle : 1:1500

Date : 09/04/2024

PC

02.c

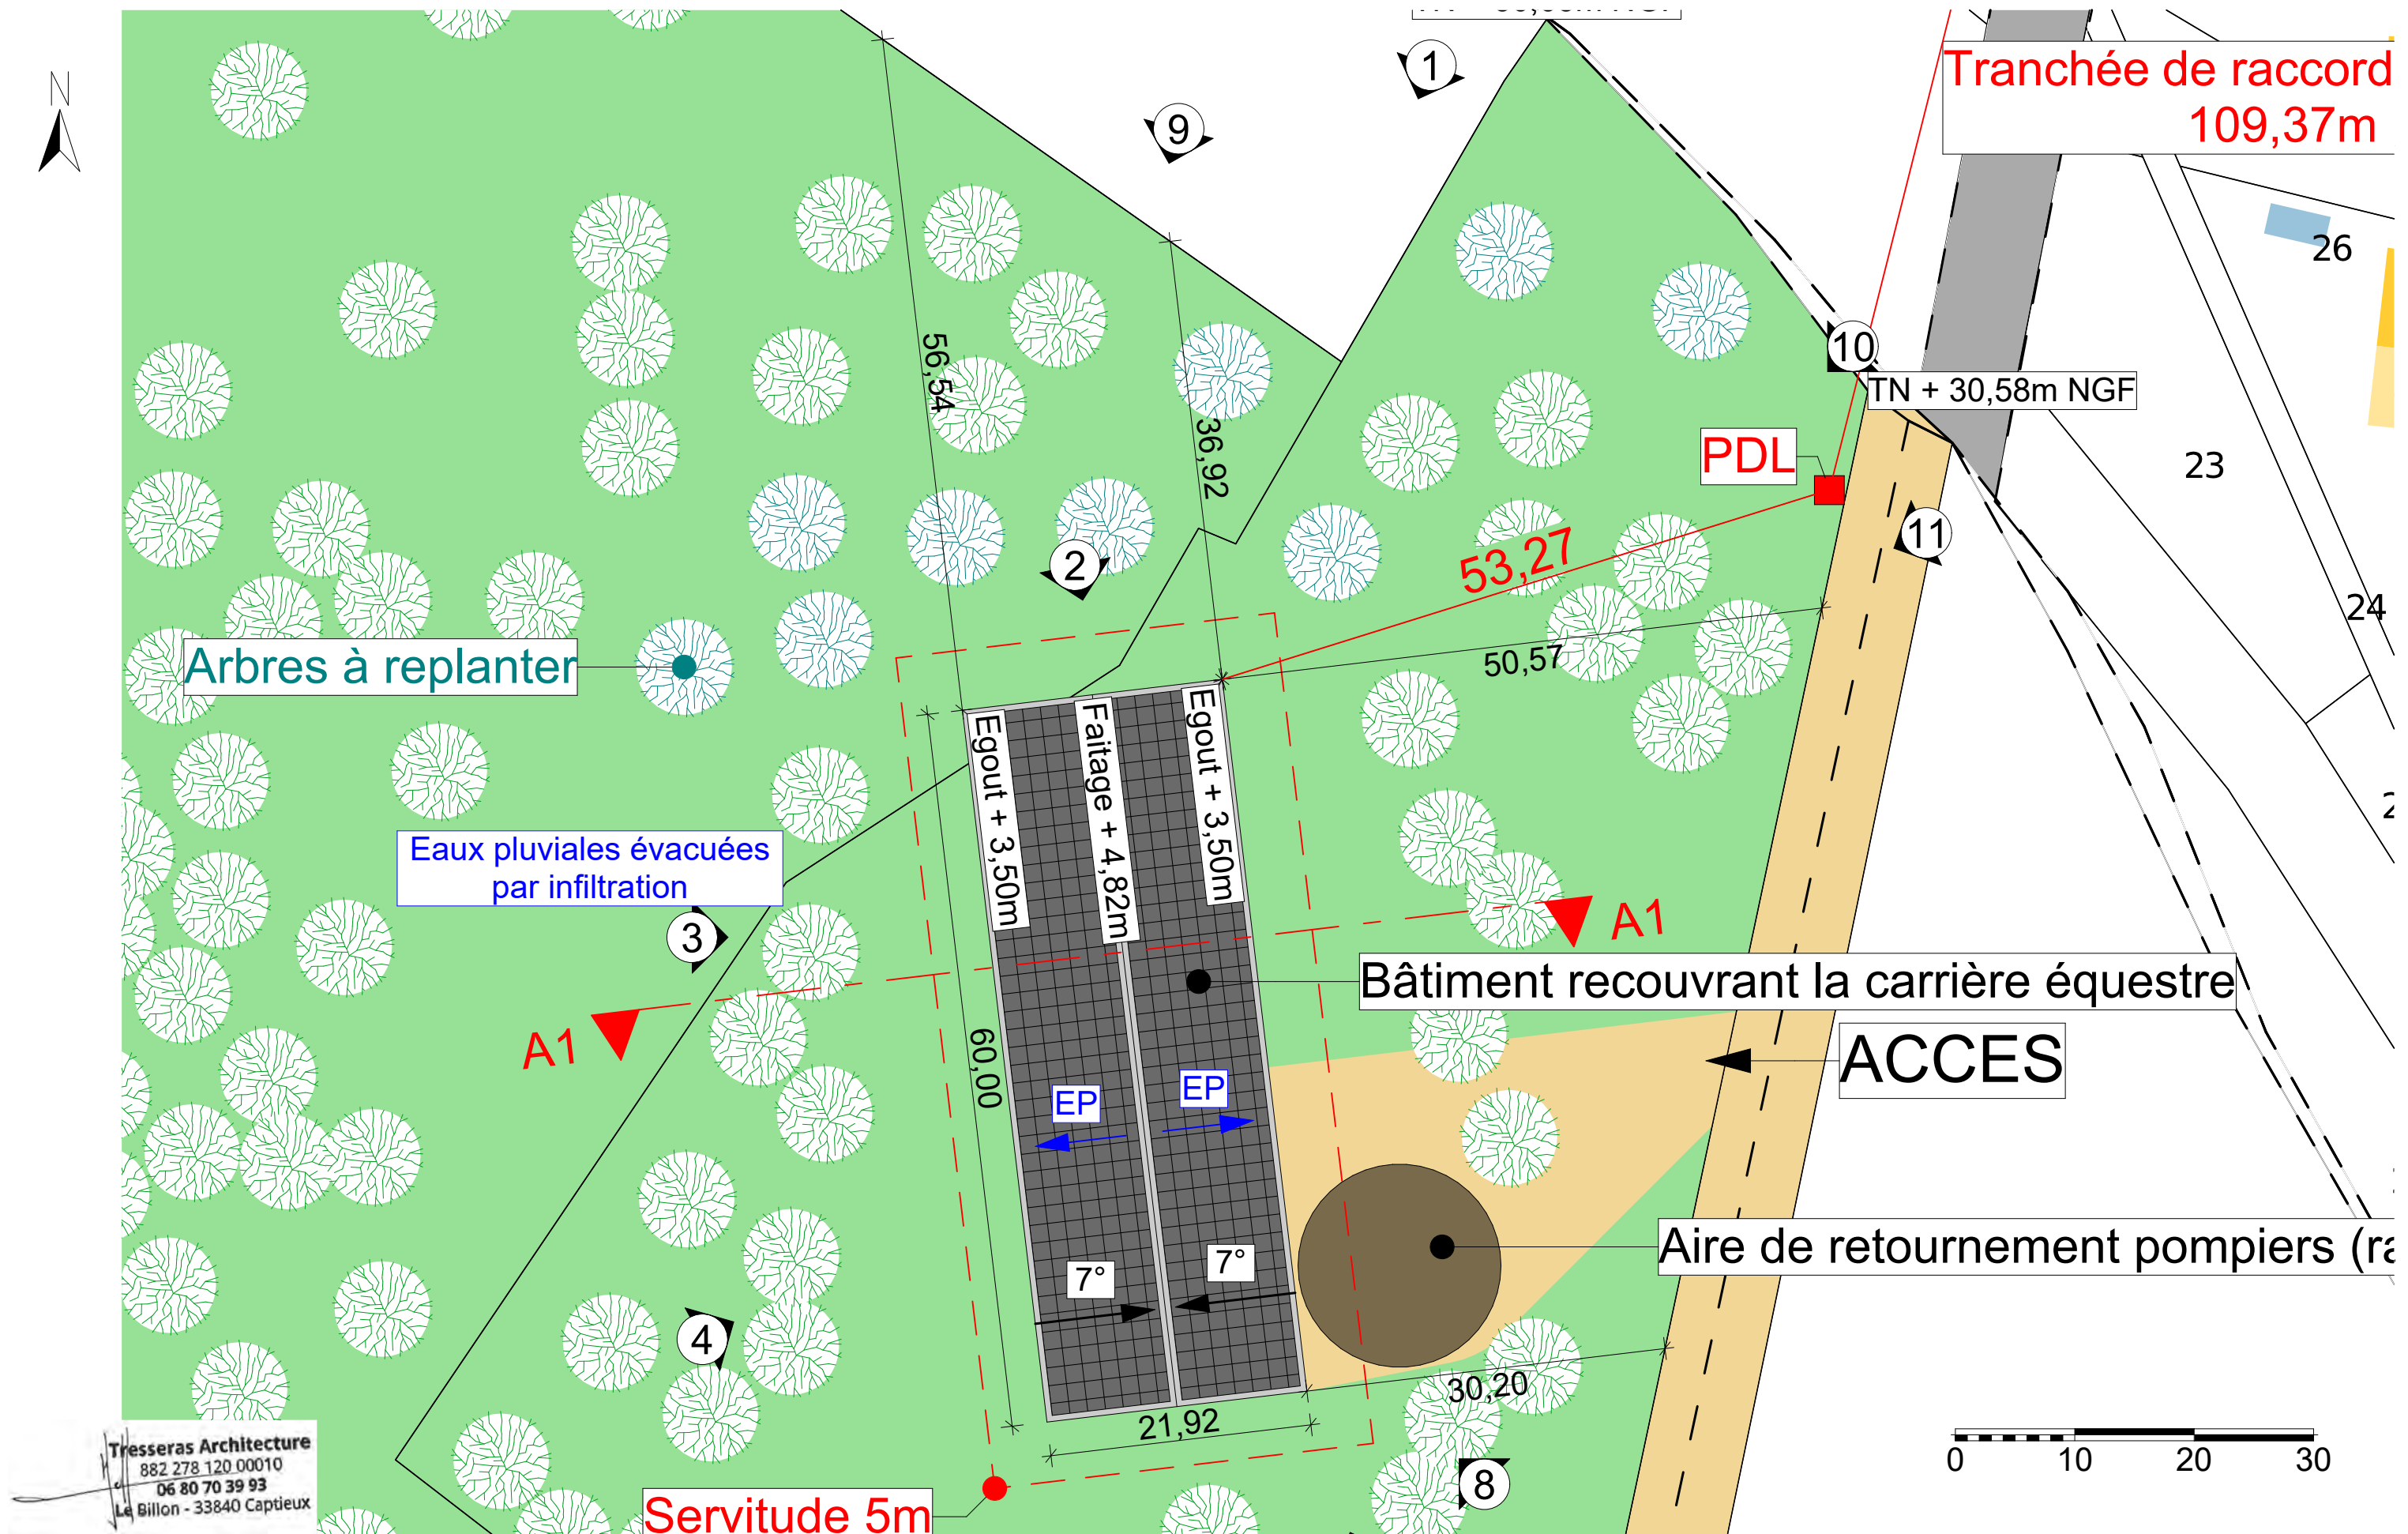

Tresseras Architecture
882 278 120 00010
06 80 70 39 93
Le Billon - 33840 Captieux

Tresseras Architecture - Siret 882 278 120 00010
Lieu dit " Le Billon " - 33840 CAPTIEUX
07 57 87 99 10 - mathieu@unarchidanslesbois



Bâtiment à usage équestre avec toiture photovoltaïque

La Grande Pièce - 33770 SALLES

ECURIE DE MYRISSE

15 Chemin de Jeantouluc - 33770 SALLES

Plan de masse état projeté (zoom)

Echelle : 1:500

Date : 09/04/2024

PC

02.d



UN ARCHI DANS LES BOIS

PC
03

NOTICE DESCRIPTIVE

1 - OBJET DE LA DEMANDE

La demande de permis de construire porte sur la construction d'un bâtiment à usage équestre avec toiture photovoltaïque. Ce bâtiment servira de manège équestre.

2 - LE SITE

Le projet se situe au lieu-dit La Grande Pièce 33770 SALLES dans le département de la Gironde. Le terrain concerné par le projet est composé d'une unité foncière n°3693, n°3697, section 000 F d'une surface totale de 35 745m². Le terrain se trouve à une altitude moyenne de 30,9 m au-dessus de la mer. Il s'inscrit dans un paysage à identité rurale. L'accès au projet se fait par un chemin privé situé à l'Est du bâtiment.

3 - LE PROJET

Le projet a pour objet la construction d'un hangar de forme rectangulaire (longueur 60m; largeur 21,92m) en structure métallique, composé de 8 travées de 7,50 mètres d'entraxe. La toiture sera constituée d'une double pente symétrique 1/2-2/2 (pente de 7°), avec pour couverture un bac acier (RAL 7016) anti condensation sur les 2 versants. Des panneaux photovoltaïques (RAL 9005) viendront recouvrir le bac acier sur les 2 versants permettant de créer une centrale de production d'électricité photovoltaïque totale de 272 kWc. Ce bâtiment sera couvert et non clos. Un terrassement sera réalisé pour la mise en œuvre d'une plateforme en grave compactée. Les eaux pluviales seront collectées par des gouttières et descentes afin d'être infiltrées sur le terrain.

4 - RACCORDEMENT AUX RESEAUX

Le bâtiment n'est pas raccordé aux réseaux d'eau, ni d'assainissement, ni d'électricité. Il n'y a donc pas de besoins en alimentation à ces niveaux là. Seule l'électricité produite par la centrale photovoltaïque est renvoyée dans le réseau ENEDIS via un point de livraison situé sur le chemin privé au Nord-Est du bâtiment (PDL). L'emplacement du point de livraison indiqué dans les pièces graphiques de l'autorisation d'urbanisme n'apparaît qu'à titre indicatif. Le positionnement du point de livraison et d'un transformateur (le cas échéant) demeure à l'appréciation finale du gestionnaire de réseau en fonction du site et des équipements déjà existants.

5 - SECURITE INCENDIE





Une borne incendie est présente à 450m du projet sur la route de Bilos, au Nord-Est du bâtiment (Cf PC 02.a - Plan de masse SDIS)

6 - VOLET PAYSAGER

Lors du projet, 9 arbres seront supprimés puis replantés sur le terrain.
L'espace pleine terre du terrain existant est de 34 489,76 m² (96,5%)
Après le projet, l'espace pleine terre sera de 33 638,15 m² (94,2%)



Les présents plans sont exclusivement destinés à l'obtention de l'autorisation administrative. Ils ne sont pas des plans d'exécution et ne peuvent en aucun cas servir à la réalisation de la construction.

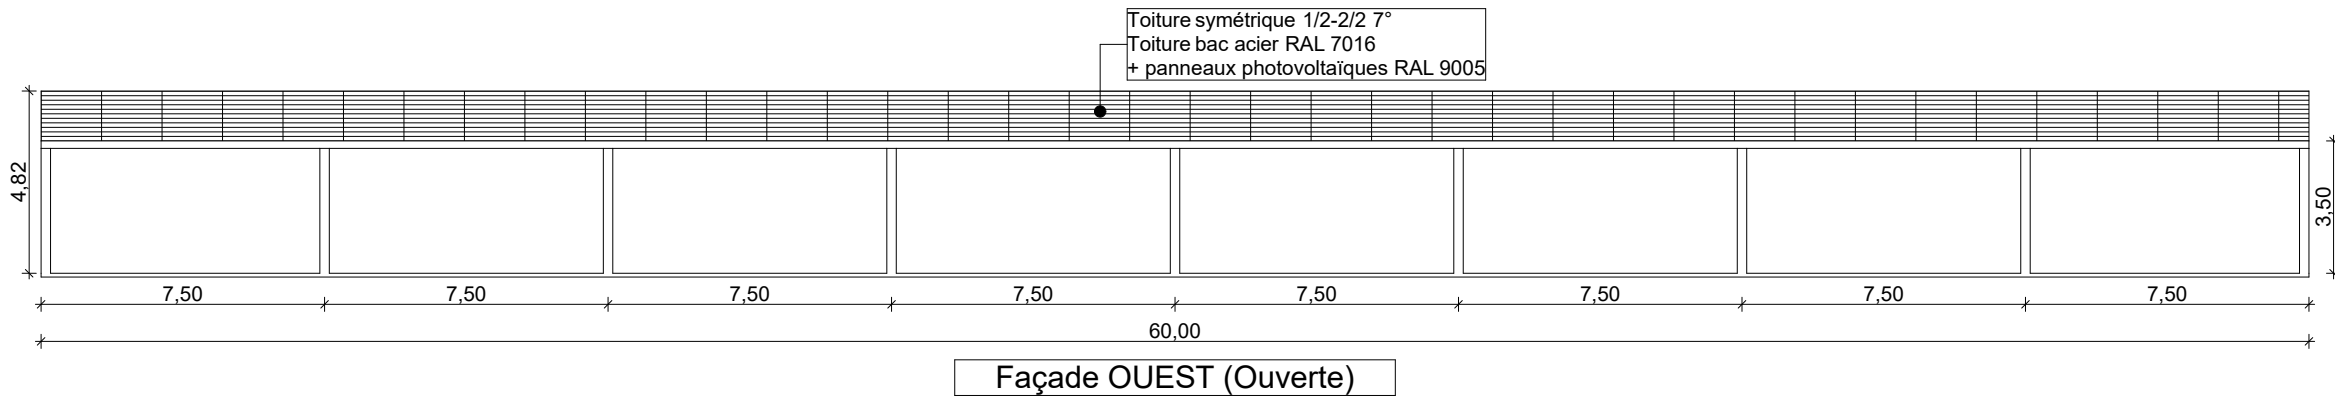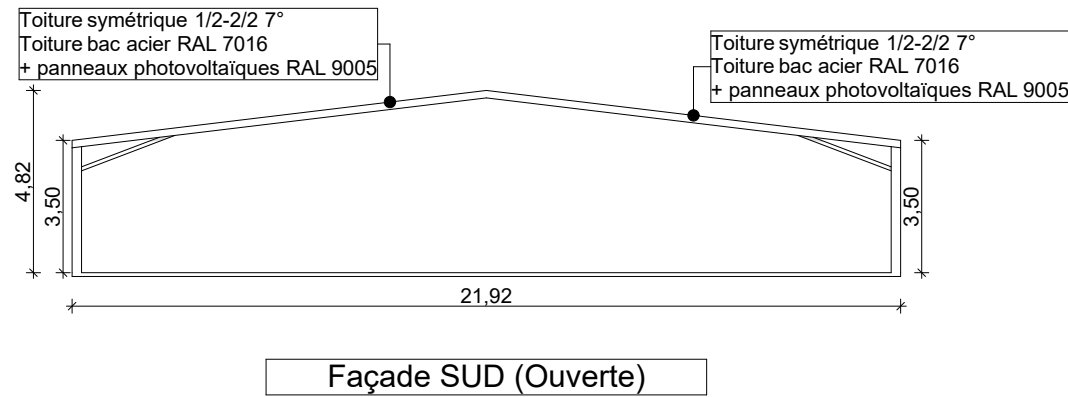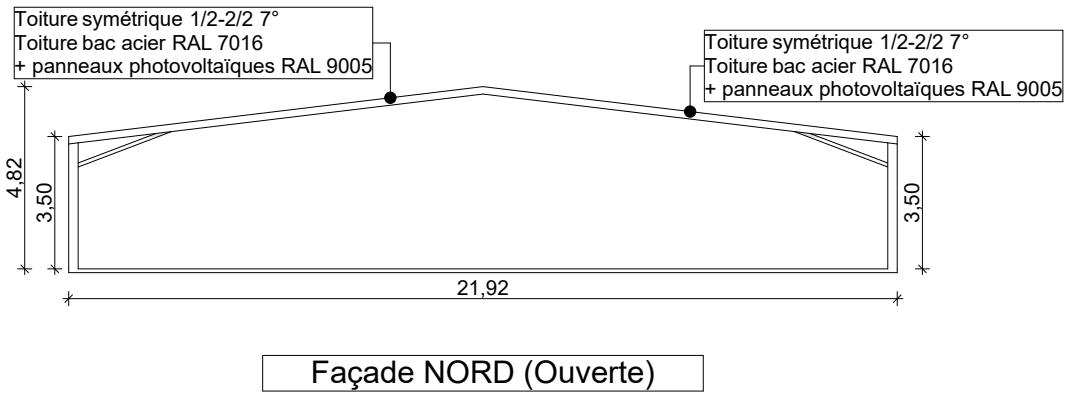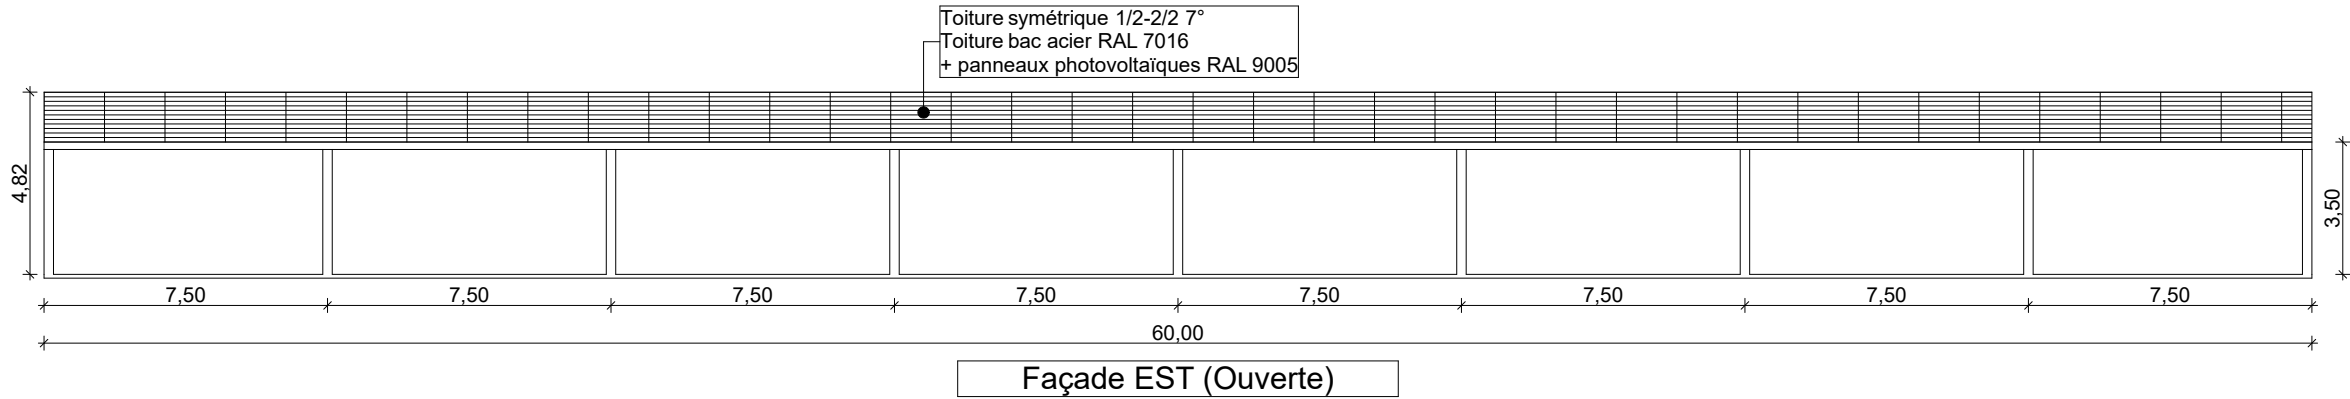

Tresseras Architecture - Siret 882 278 120 00010
Lieu dit " Le Billon " - 33840 CAPTIEUX
07 57 87 99 10 - mathieu@unarchidanslesbois



Bâtiment à usage équestre avec toiture photovoltaïque

La Grande Pièce - 33770 SALLES

ECURIE DE MYRISSE
15 Chemin de Jeantouluc - 33770 SALLES


Plan de façades

Echelle : 1:200

Date : 09/04/2024

PC
05.a

Les présents plans sont exclusivement destinés à l'obtention de l'autorisation administrative. Ils ne sont pas des plans d'exécution et ne peuvent en aucun cas servir à la réalisation de la construction.

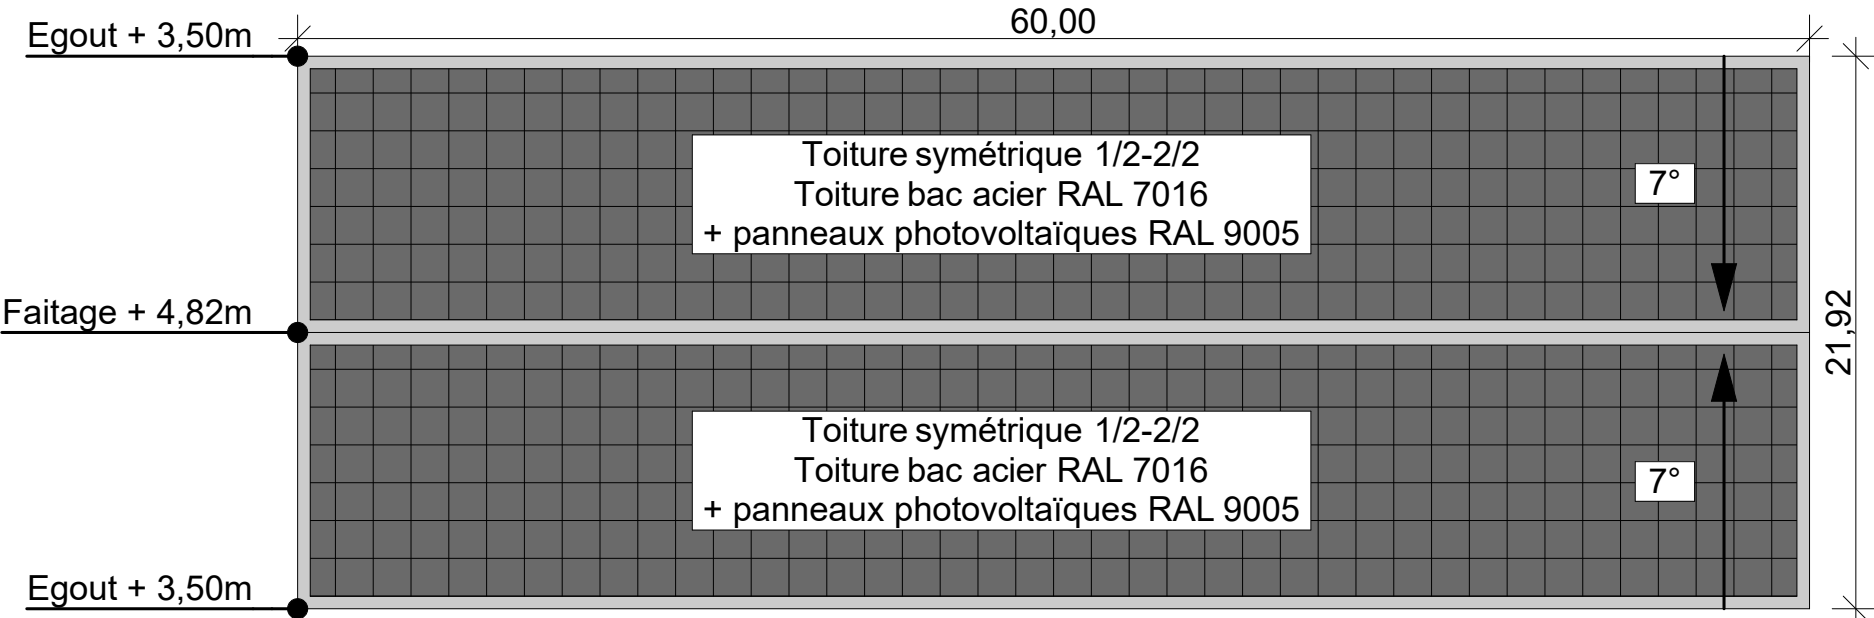

Tresseras Architecture - Siret 882 278 120 00010
Lieu dit " Le Billon " - 33840 CAPTIEUX
07 57 87 99 10 - mathieu@unarchidanslesbois.is



Bâtiment à usage équestre avec toiture photovoltaïque

La Grande Pièce - 33770 SALLES
ECURIE DE MYRISSE
15 Chemin de Jeantouluc - 33770 SALLES

Plan de toiture
Echelle : 1:300
Date : 09/04/2024



AVANT PROJET



APRES PROJET

Tresseras Architecture
882 278 120 00010
06 80 70 39 93
Le Billon - 33840 Captieux

Tresseras Architecture - Siret 882 278 120 00010
Lieu dit " Le Billon " - 33840 CAPTIEUX
07 57 87 99 10 - mathieu@unarchidanslesbois



Bâtiment à usage équestre avec toiture photovoltaïque

La Grande Pièce - 33770 SALLES

ECURIE DE MYRISSE

15 Chemin de Jeantoulic - 33770 SALLES

Insertion paysagère

Echelle :

Date : 09/04/2024

PC

06

Les présents plans sont exclusivement destinés à l'obtention de l'autorisation administrative. Ils ne sont pas des plans d'exécution et ne peuvent en aucun cas servir à la réalisation de la construction.

PHOTO 1



PHOTO 2



PHOTO 3



PHOTO 4



PHOTO 5



PHOTO 6



Tresseras Architecture
882 278 120 00010
06 80 70 39 93
Le Billon - 33840 Captieux

Tresseras Architecture - Siret 882 278 120 00010
Lieu dit " Le Billon " - 33840 CAPTIEUX
07 57 87 99 10 - mathieu@unarchidanslesbois



Bâtiment à usage équestre avec toiture photovoltaïque

La Grande Pièce - 33770 SALLES

ECURIE DE MYRISSE

15 Chemin de Jeantouluc - 33770 SALLES

Documents photographiques

Date : 09/04/2024

PC

07

Les présents plans sont exclusivement destinés à l'obtention de l'autorisation administrative. Ils ne sont pas des plans d'exécution et ne peuvent en aucun cas servir à la réalisation de la construction.

PHOTO 7



PHOTO 8



PHOTO 9



PHOTO 10



PHOTO 11



Tresseras Architecture
882 278 120 00010
06 80 70 39 93
Le Billon - 33840 Captieux

Tresseras Architecture - Siret 882 278 120 00010
Lieu dit " Le Billon " - 33840 CAPTIEUX
07 57 87 99 10 - mathieu@unarchidanslesbois



Bâtiment à usage équestre avec toiture photovoltaïque

La Grande Pièce - 33770 SALLES

ECURIE DE MYRISSE

15 Chemin de Jeantouluc - 33770 SALLES


Documents photographiques

Date : 09/04/2024

PC

08

Les présents plans sont exclusivement destinés à l'obtention de l'autorisation administrative. Ils ne sont pas des plans d'exécution et ne peuvent en aucun cas servir à la réalisation de la construction.

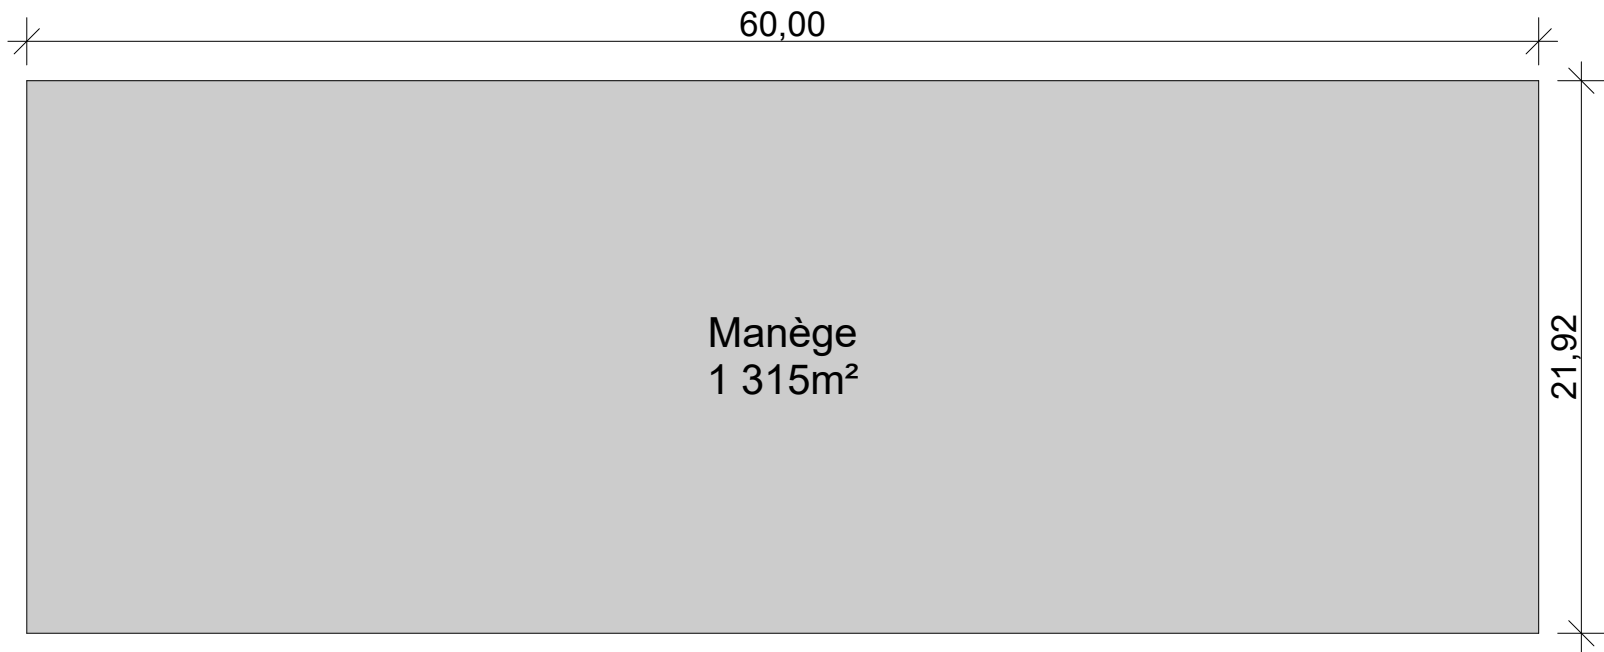

Tresseras Architecture - Siret 882 278 120 00010
Lieu dit " Le Billon " - 33840 CAPTIEUX
07 57 87 99 10 - mathieu@unarchidanslesbois



Bâtiment à usage équestre avec toiture photovoltaïque
La Grande Pièce - 33770 SALLES
ECURIE DE MYRISSE
15 Chemin de Jeantoulic - 33770 SALLES

Plan d'aménagement intérieur
Echelle : 1:300
Date : 09/04/2024





UN ALCOOL DANS LES BOIS

15 Chemin de Jeantoulic - 33770 SALLES

Date : 09/04/2024

PC
ANNEXE