

PERMIS DE CONSTRUIRE

- ☑ PAGE DE GARDE
- ☑ PC 01.a - PLAN DE SITUATION (carte IGN)
PC 01.b - PLAN DE SITUATION (plan cadastral)
PC 01.c - PLAN DE SITUATION (vue aérienne)
- ☑ PC 02.a - PLAN DE MASSE EDL
PC 02.b - PLAN DE MASSE PROJET
PC 02.c - PLAN DE MASSE ZOOM
- ☑ PC 03 - COUPE DE TERRAIN
- ☑ PC 04 - NOTICE D'INSERTION
- ☑ PC 05.a - PLAN DE FACADES
PC 05.b - PLAN DE TOITURE
- ☑ PC 06 - INSERTION PAYSAGÈRE
- ☑ PC 07/08 - DOCUMENTS PHOTOGRAPHIQUES
- ☑ ANNEXE - COORDONNEES SEXAGESIMALES

Bâtiment à usage agricole avec toiture photovoltaïque

Maître d'ouvrage :

EARL SAINT SAUVEUR

Quartier Cayron A Cabeil
32160 BEAUMARCHES

Adresse du projet :

Lieu-dit Cayron
32160 BEAUMARCHES



- Section 000 D 266
Superficie 14 360m²



UN ARCHIT DANS LES BOIS®

Tresseras Architecture
882 278 120 00010
06 80 70 39 93
Le Billon - 33840 Captieux

Tresseras Architecture - Siret 882 278 120 00010
Lieu dit " Le Billon " - 33840 CAPTIEUX
07 57 87 99 10 - mathieu@unarchidanslesbo.is

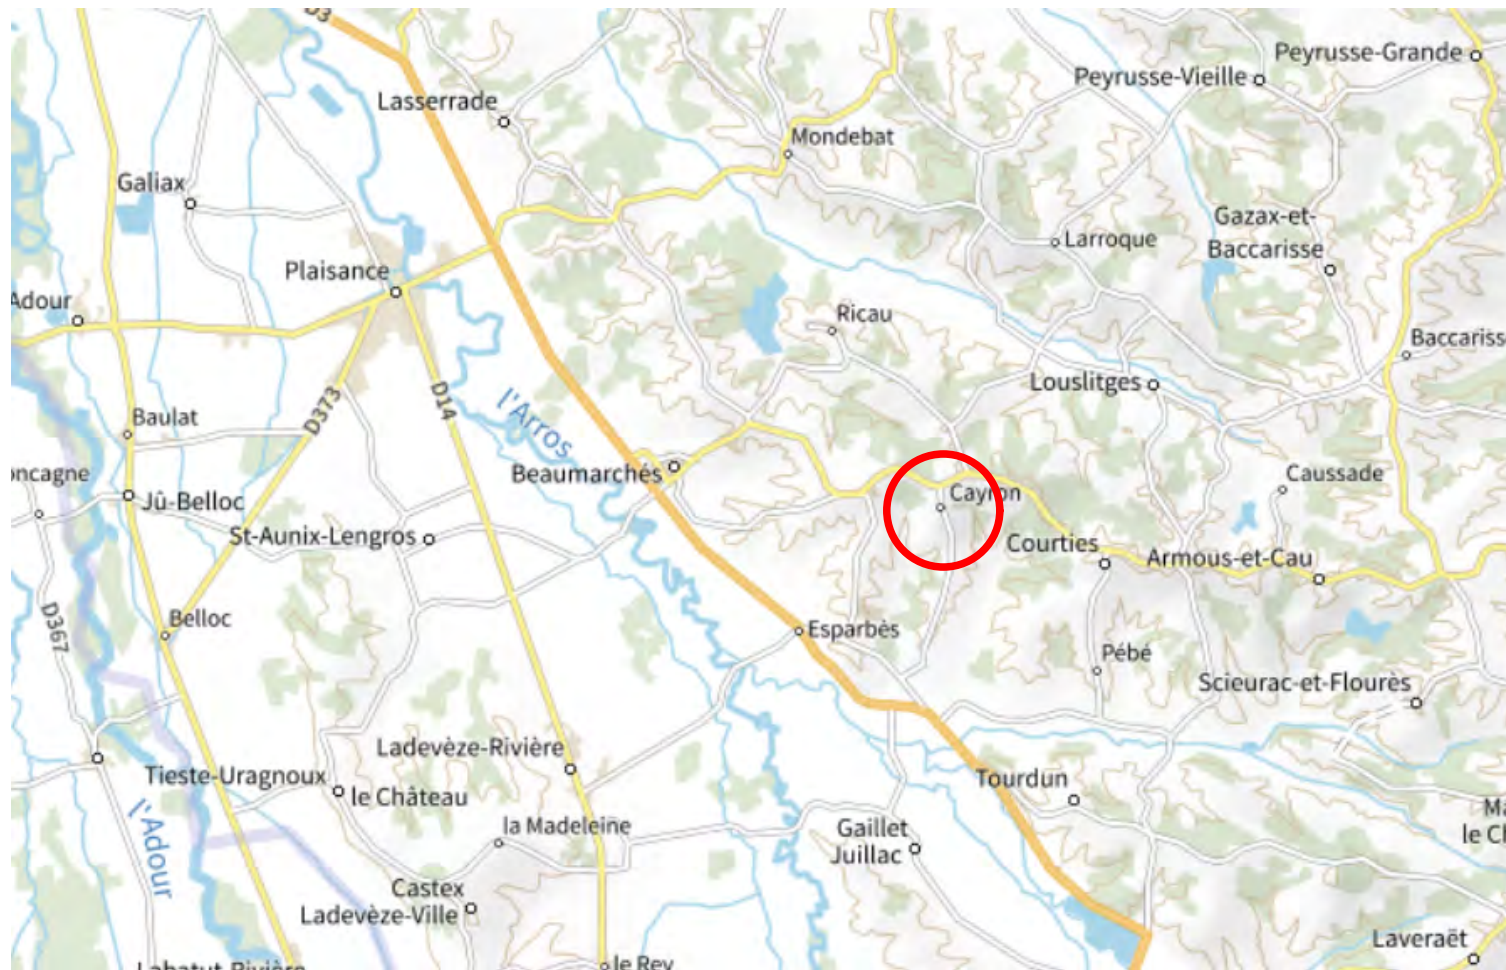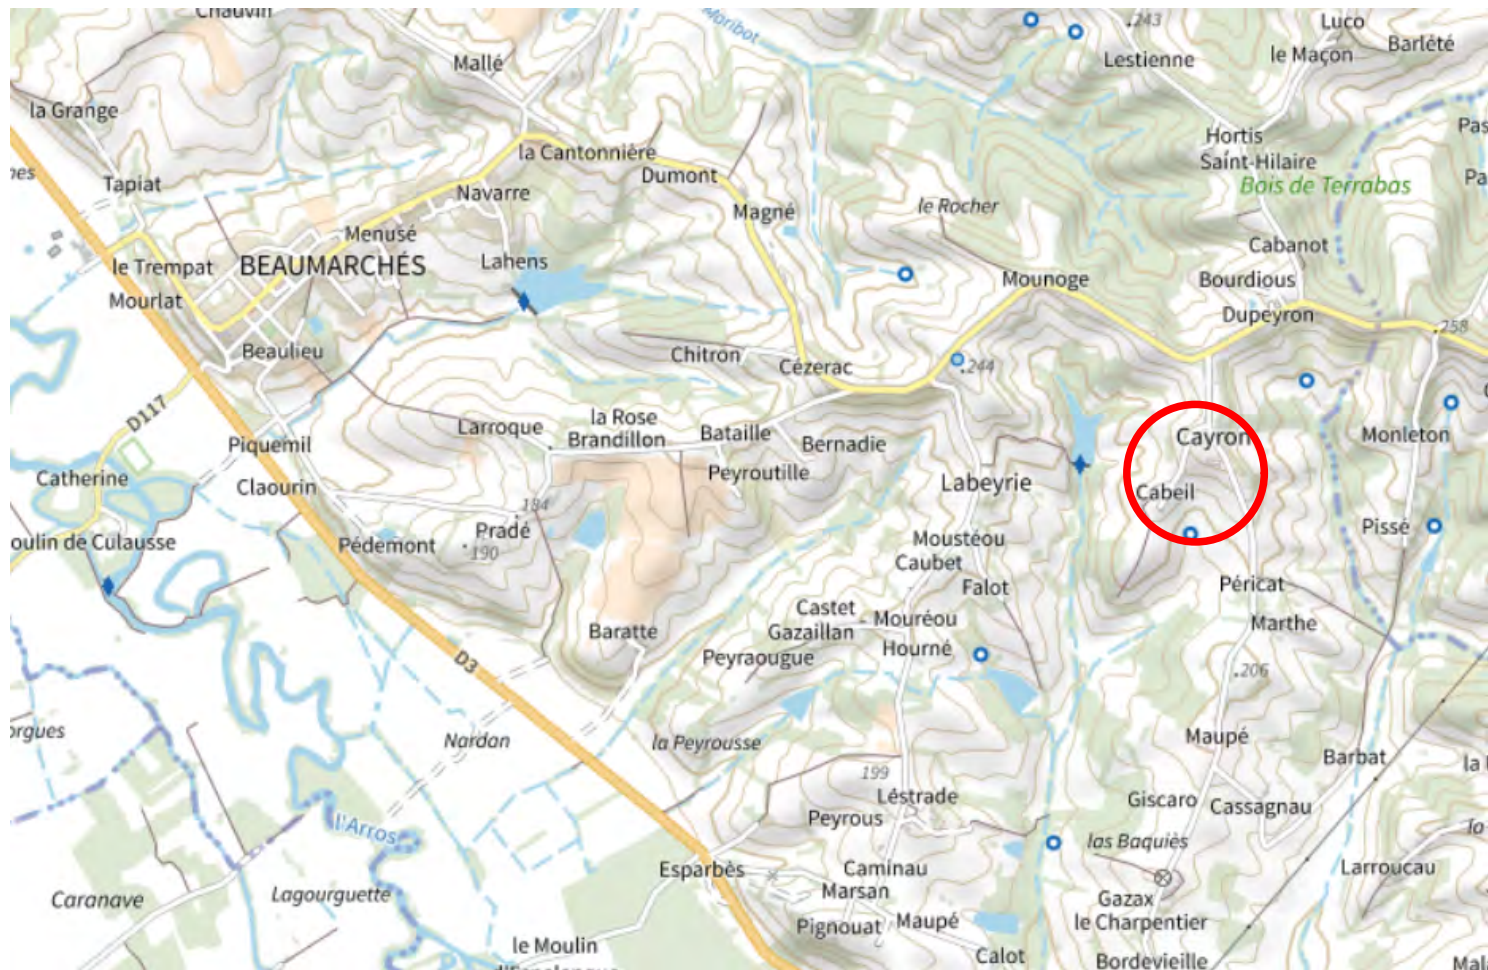

Tresseras Architecture - Siret 882 278 120 00010
Lieu dit " Le Billon " - 33840 CAPTIEUX
07 57 87 99 10 - mathieu@unarchidanslesbo.is

Bâtiment à usage agricole avec toiture photovoltaïque


Lieu-dit Cayron 32160 BEAUMARCHES
EARL SAINT SAUVEUR
Quartier Cayron A Cabel 32160 BEAUMARCHES



Plan de situation (carte IGN)
Echelle :
Date :04/01/2024

PC
-01.a-

Les présents plans sont exclusivement destinés à l'obtention de l'autorisation administrative. Ils ne sont pas des plans d'exécution et ne peuvent en aucun cas servir à la réalisation de la construction.

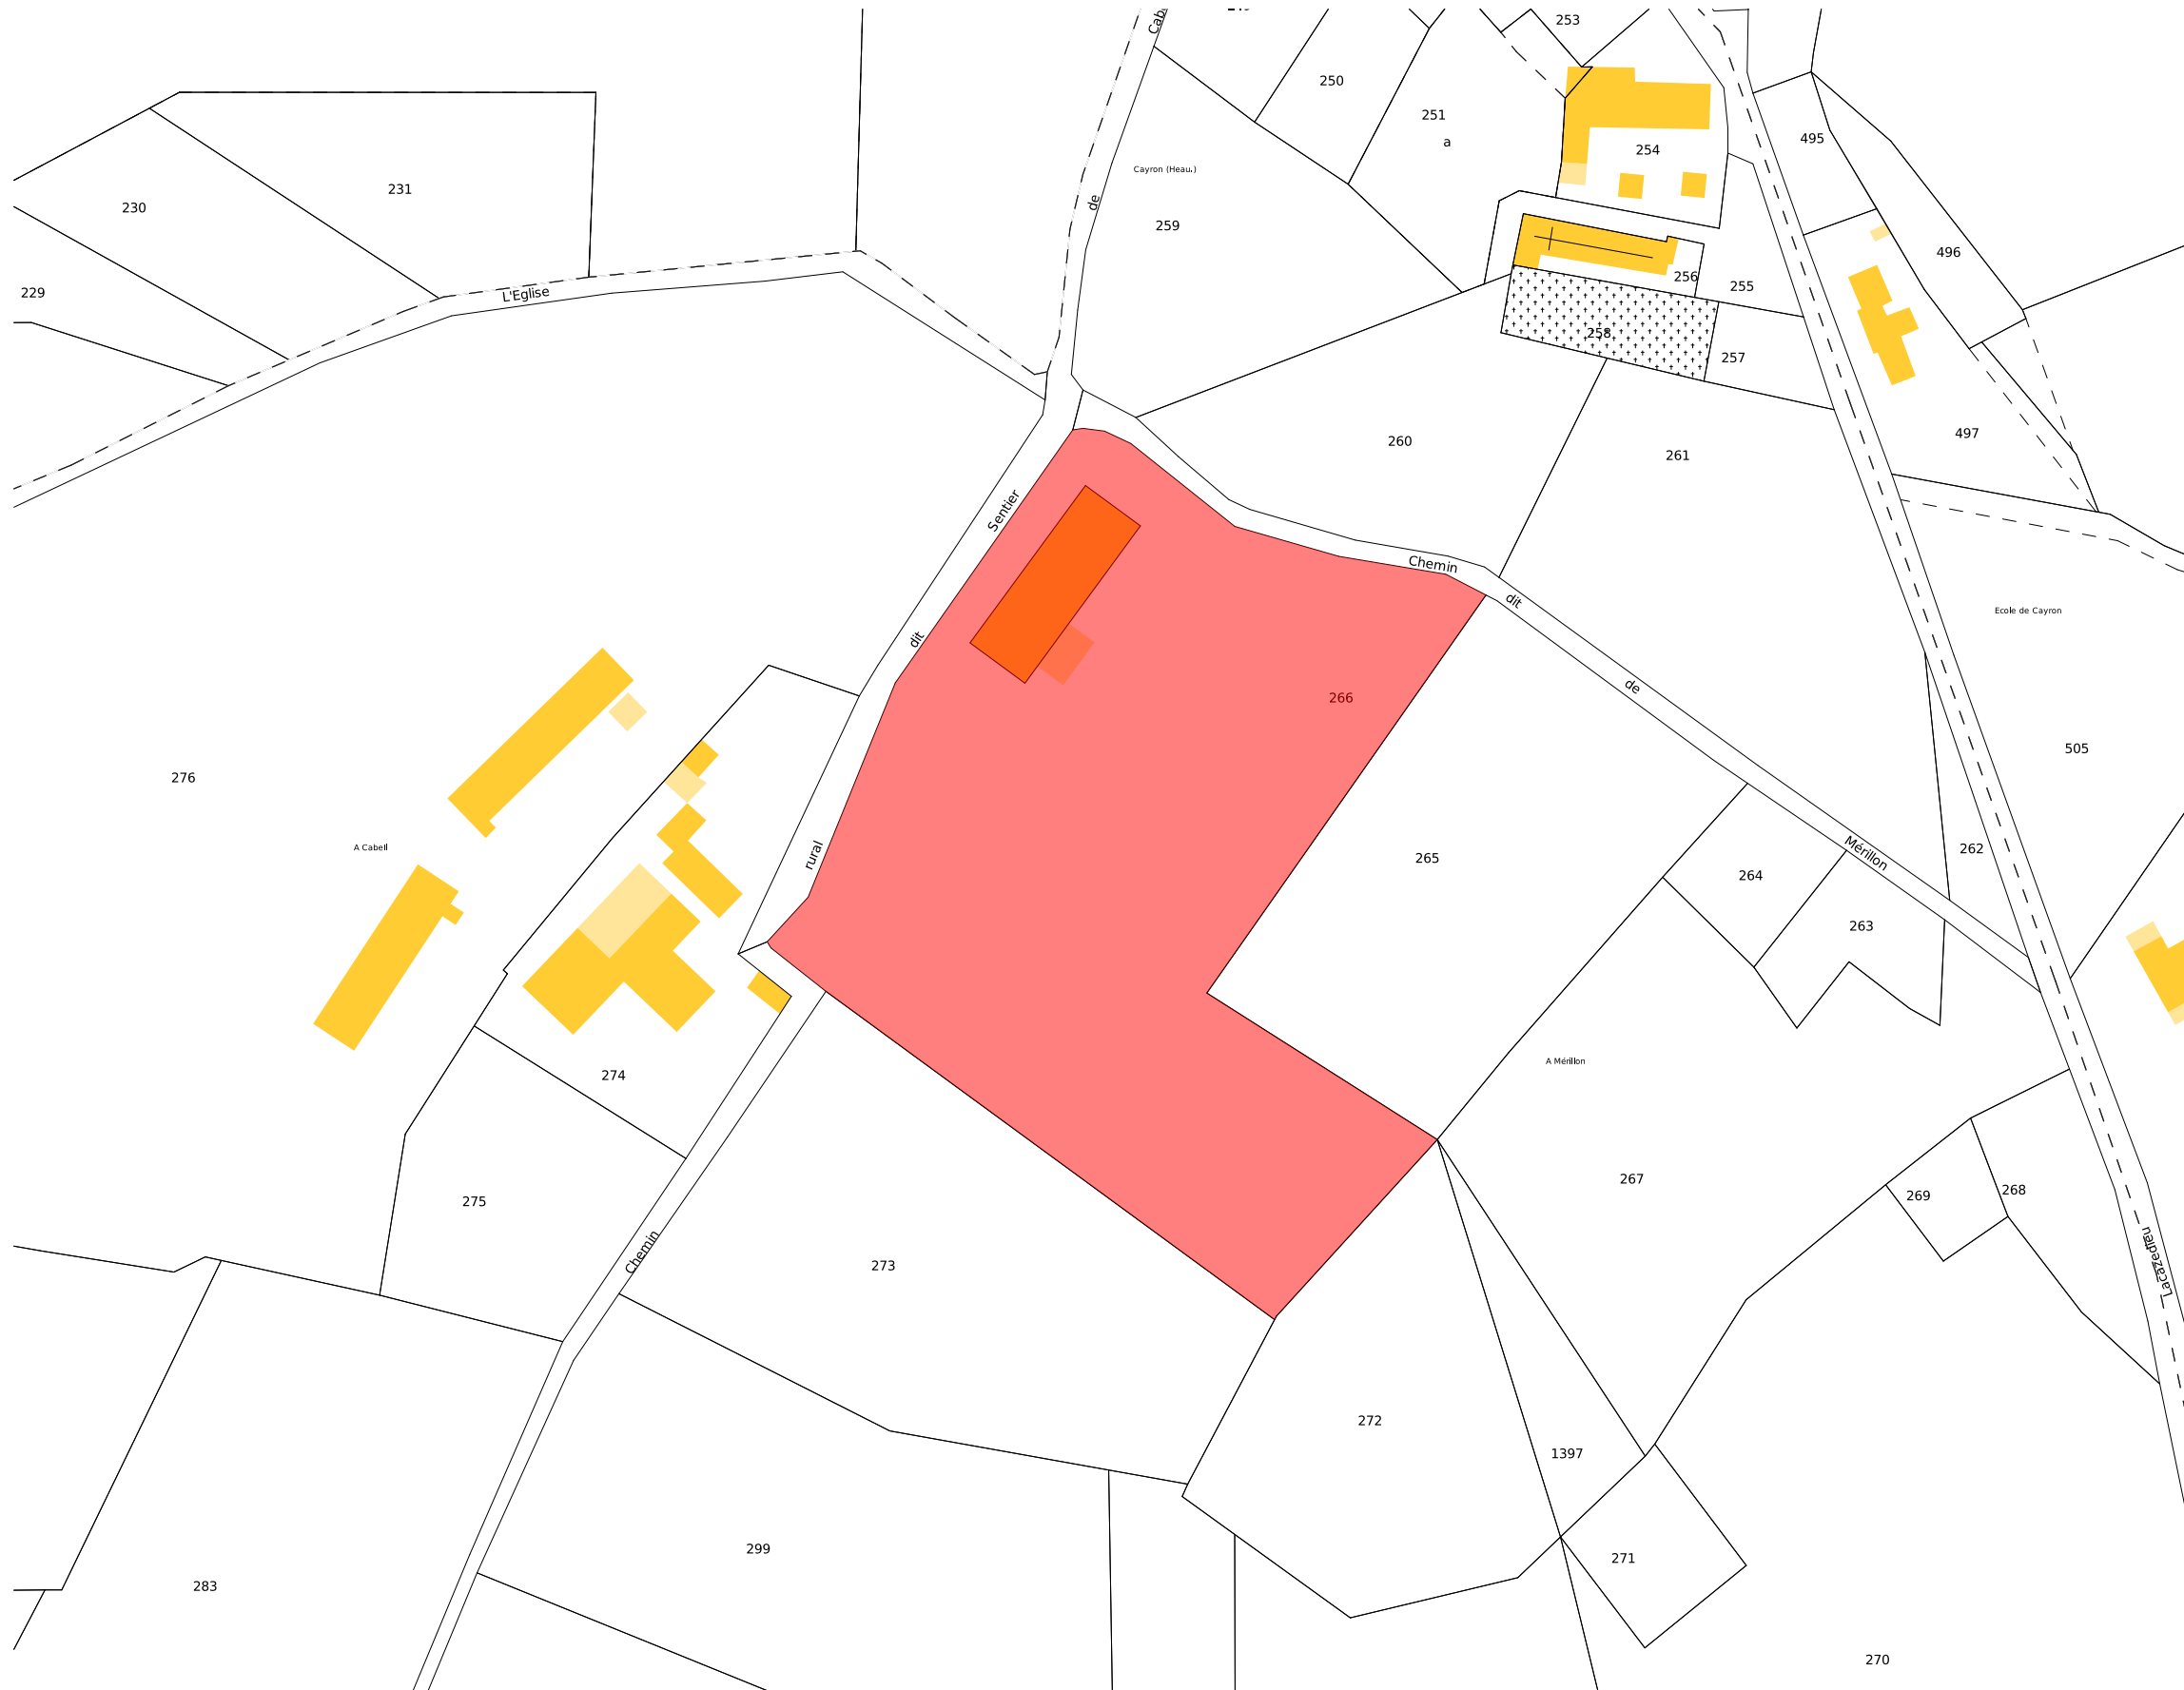

Tresseras Architecture - Siret 882 278 120 00010
Lieu-dit " Le Billon " - 33840 CAPTIEUX
07 57 87 99 10 - mathieu@unarchidanslesbo.is

Bâtiment à usage agricole avec toiture photovoltaïque

Lieu-dit Cayron 32160 BEAUMARCHES

EARL SAINT SAUVEUR

Quartier Cayron A Cabeil 32160 BEAUMARCHES




Plan de situation
(plan cadastral)

Echelle : 1:1500

Date :04/01/2024

PC
-01.b-

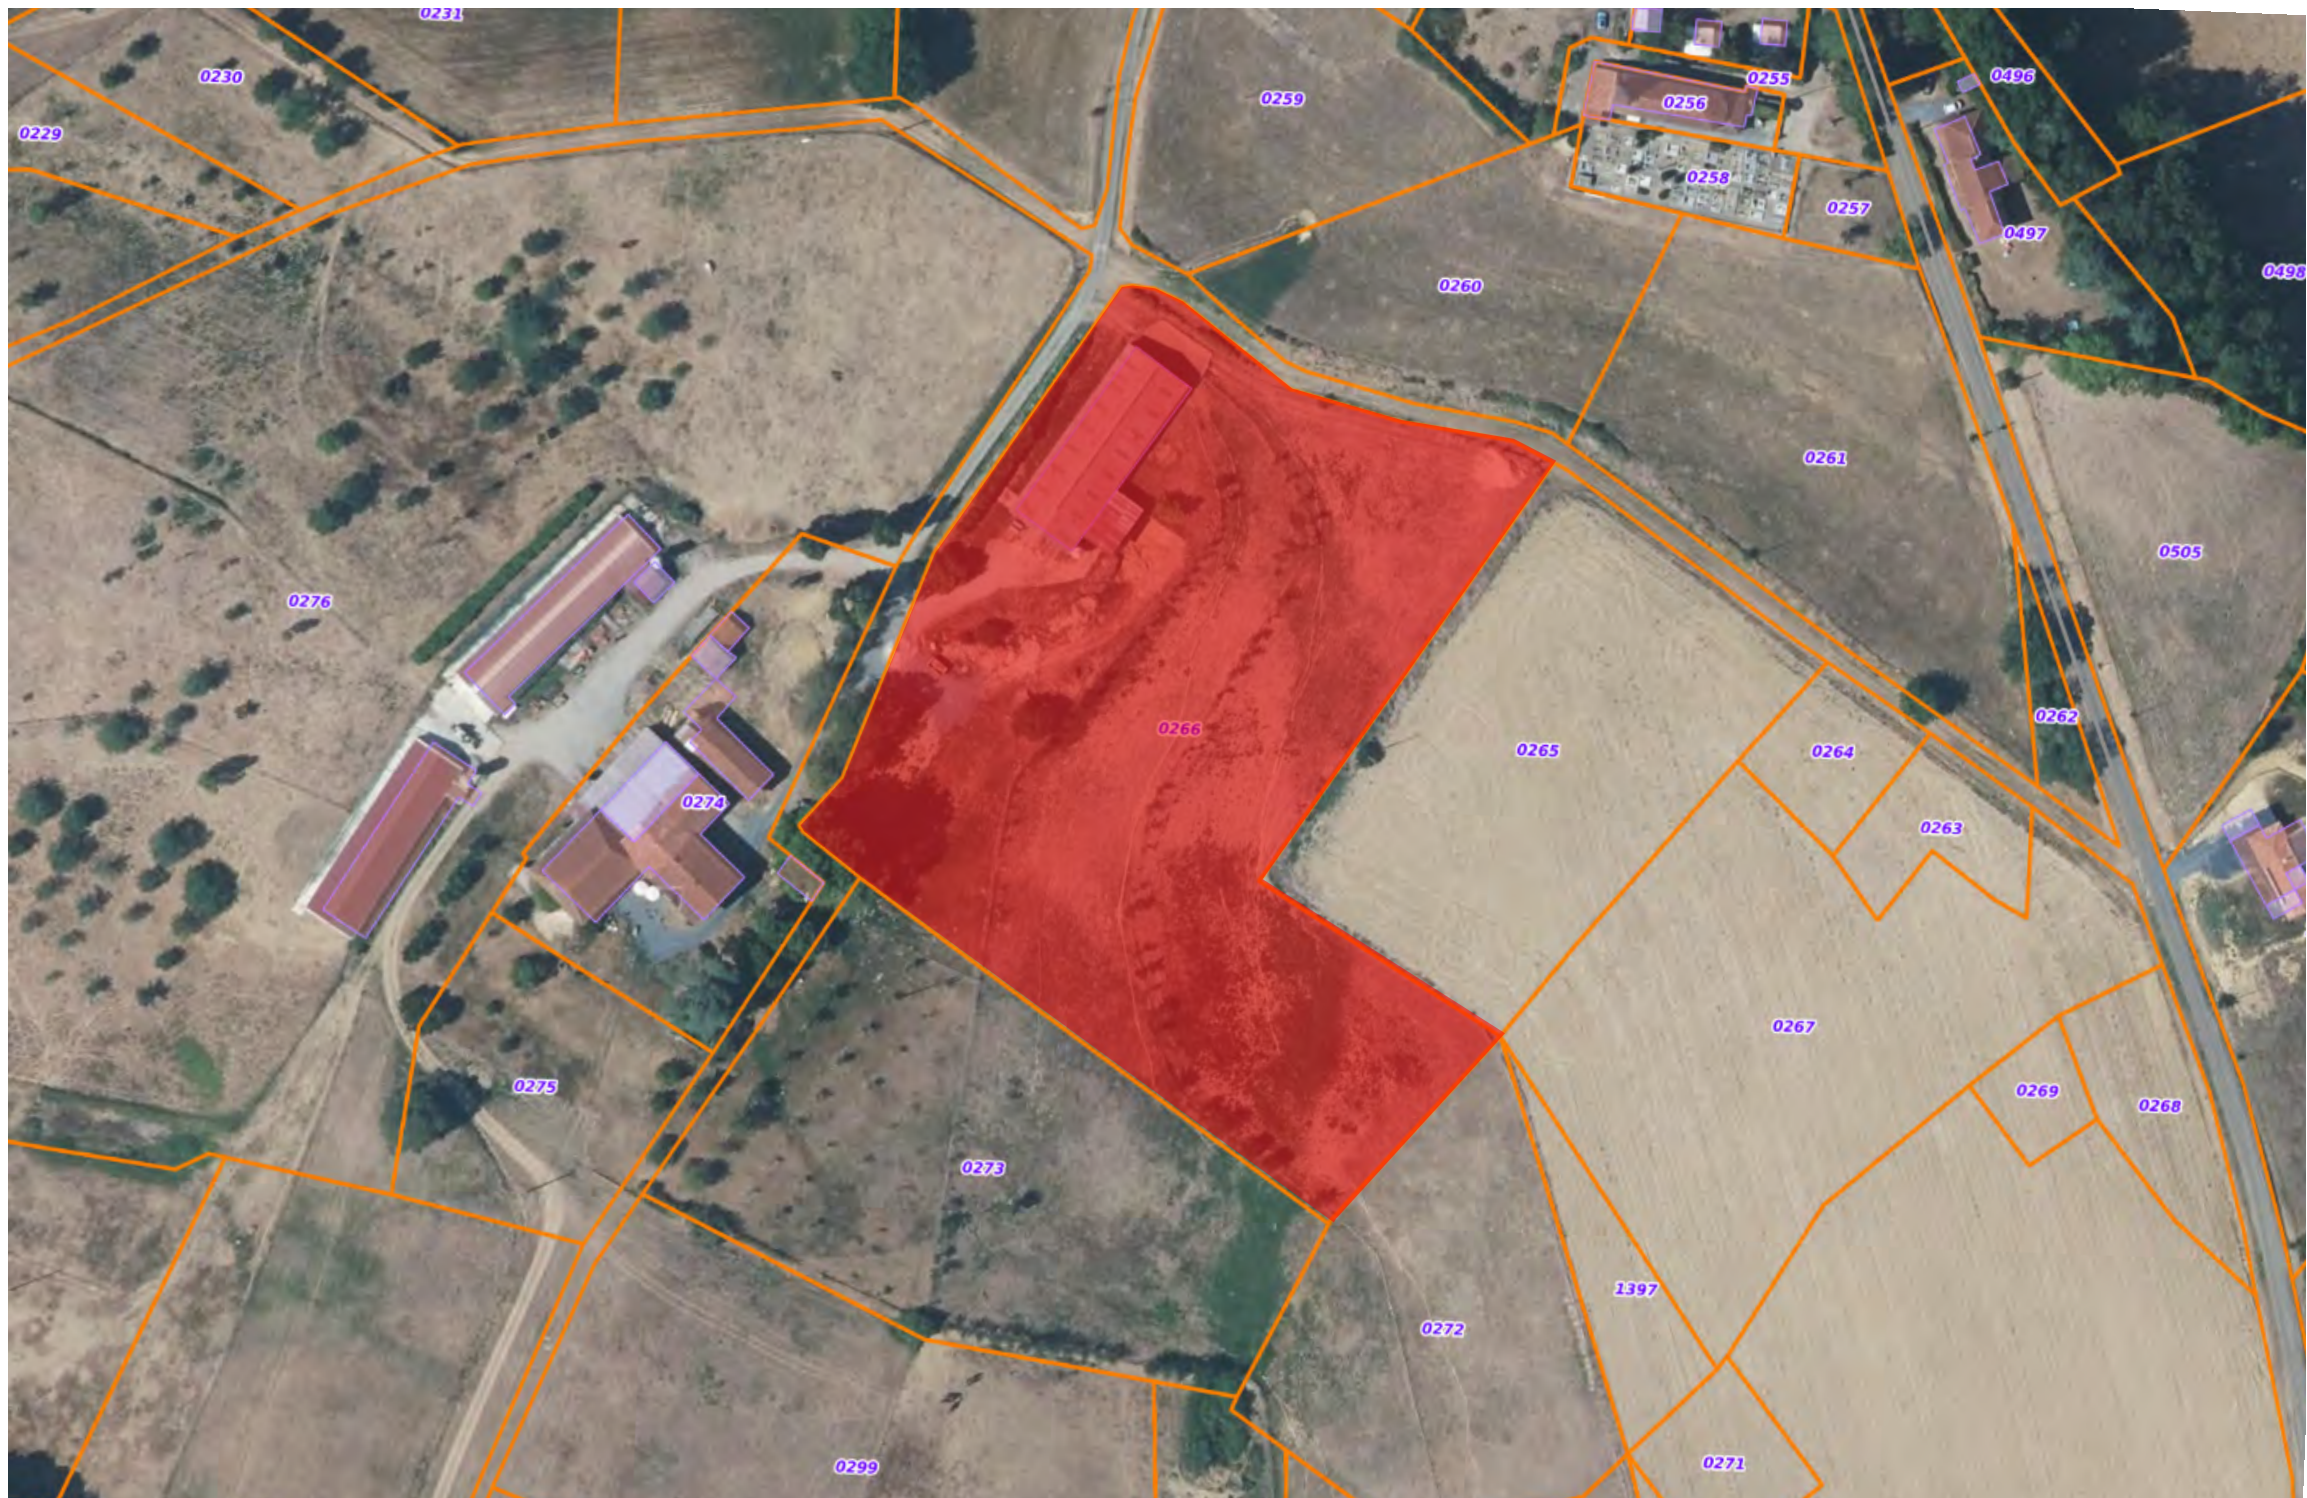


Tresseras Architecture - Siret 882 278 120 00010
Lieu dit " Le Billon " - 33840 CAPTIEUX
07 57 87 99 10 - mathieu@unarchidanslesbo.is

Bâtiment à usage agricole avec toiture photovoltaïque
Lieu-dit Cayron 32160 BEAUMARCHES
EARL SAINT SAUVEUR
Quartier Cayron A Cabeil 32160 BEAUMARCHES



Plan de situation
(vue aérienne)
Echelle : 1:1500
Date :04/01/2024

PC
-01.c-

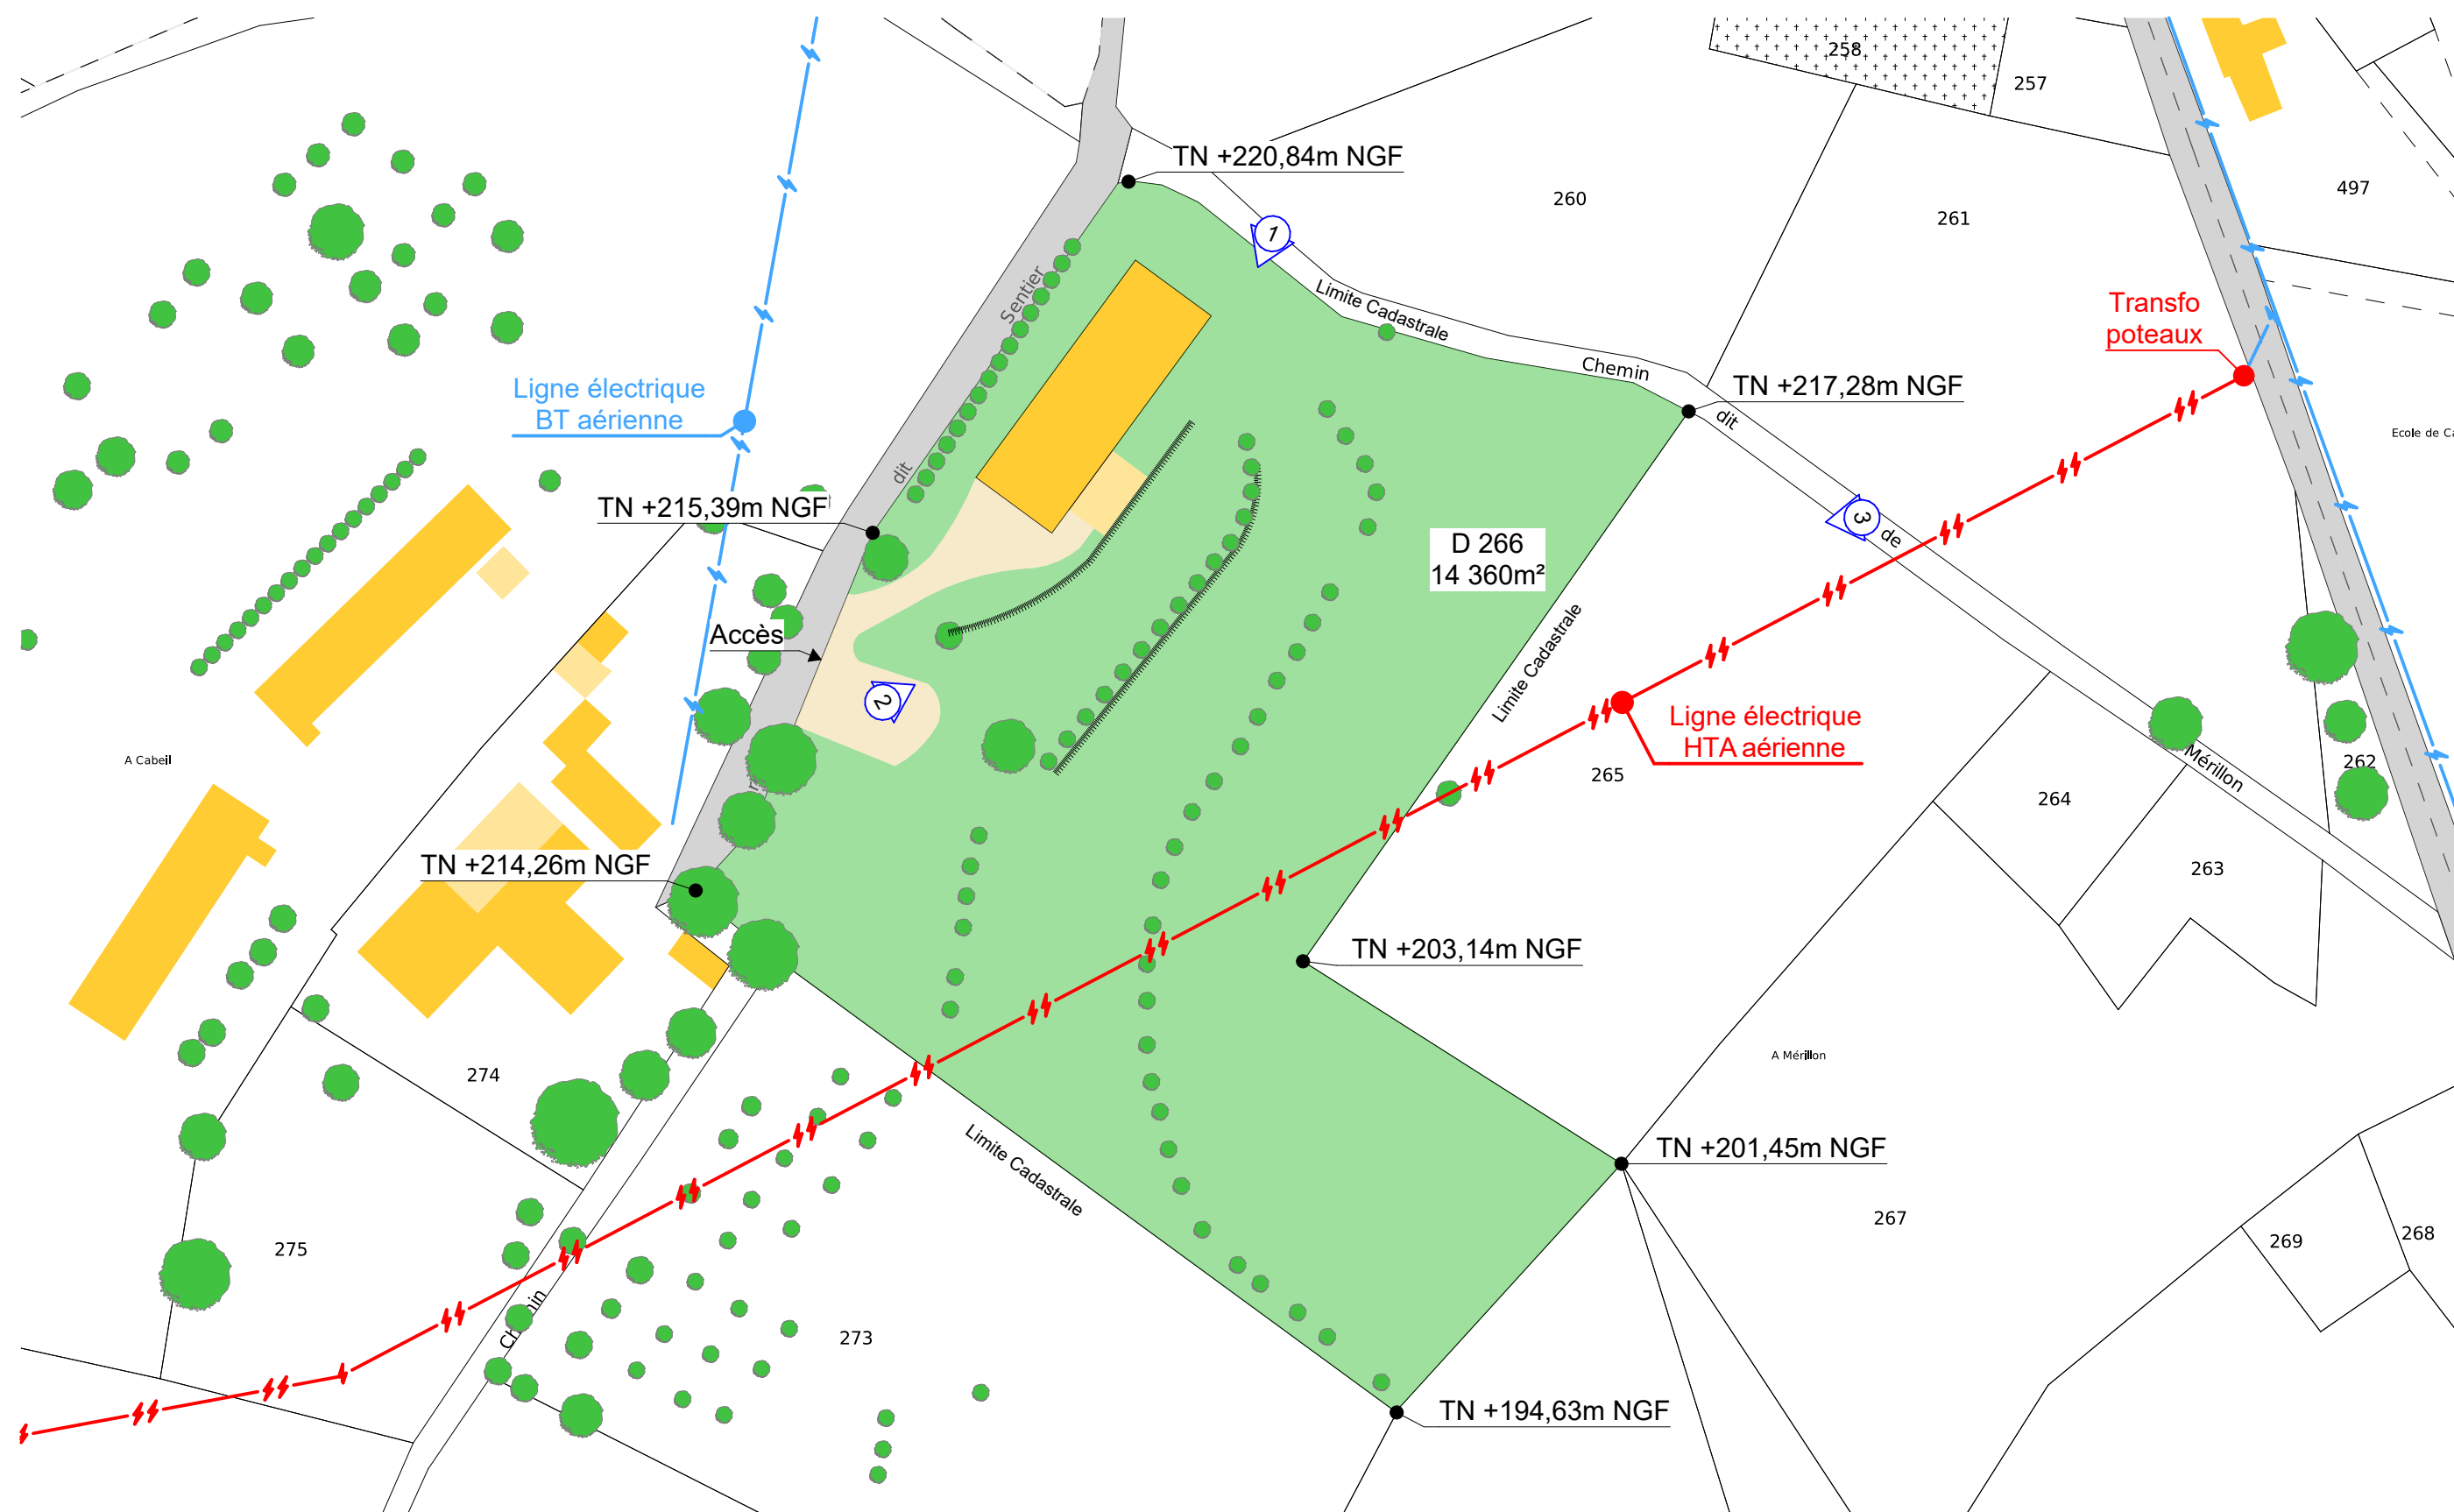

Tresseras Architecture - Siret 882 278 120 00010
Lieu-dit " Le Billon " - 33840 CAPTIEUX
07 57 87 99 10 - mathieu@unarchidanslesbo.is

Bâtiment à usage agricole avec toiture photovoltaïque

Lieu-dit Cayron 32160 BEAUMARCHES
EARL SAINT SAUVEUR
Quartier Cayron A Cabel 32160 BEAUMARCHES



Plan de masse EDL
Echelle : 1:1000
Date :04/01/2024


PC
-02.a-



Tresseras Architecture
882 278 120 00010
06 80 70 39 93
Le Billon - 33840 Captieux

PC
-02.b-

Les présents plans sont exclusivement destinés à l'obtention de l'autorisation administrative. Ils ne sont pas des plans d'exécution et ne peuvent en aucun cas servir à la réalisation de la construction.

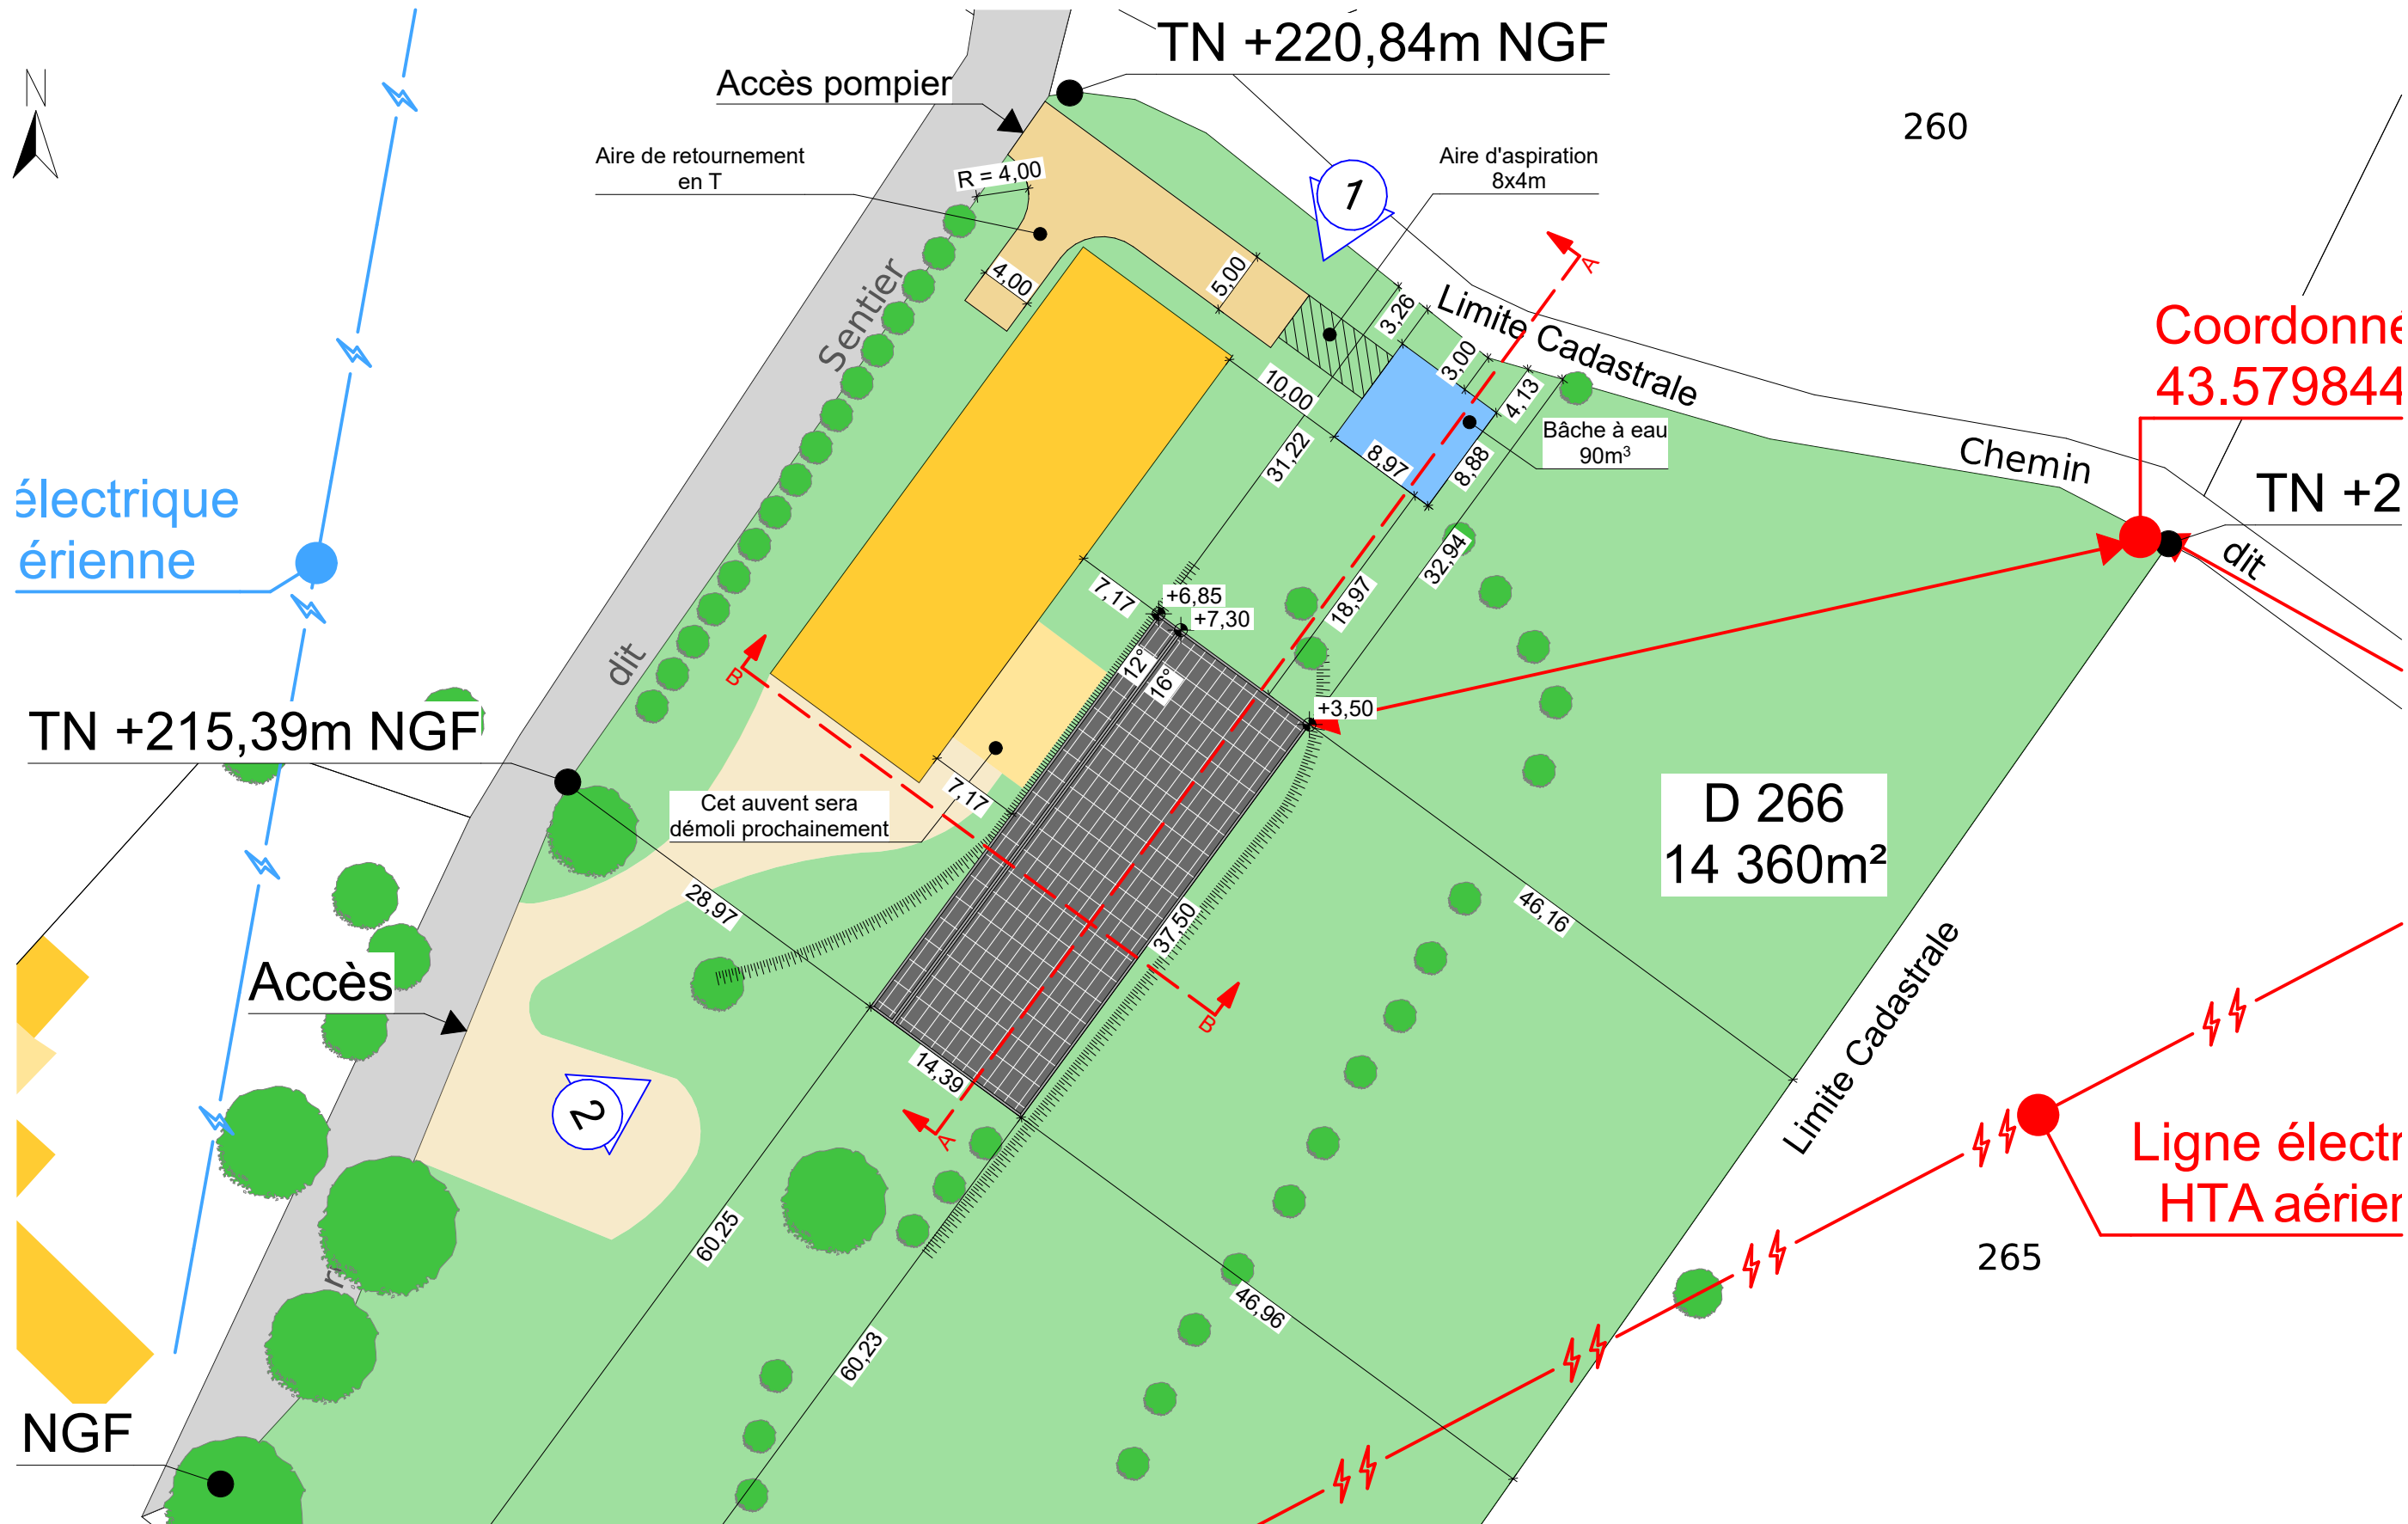

Tresseras Architecture - Siret 882 278 120 00010
Lieu dit " Le Billon " - 33840 CAPTIEUX
07 57 87 99 10 - mathieu@unarchidanslesbo.is

Bâtiment à usage agricole avec toiture photovoltaïque

Lieu-dit Cayron 32160 BEAUMARCHES
EARL SAINT SAUVEUR
Quartier Cayron A Cabeil 32160 BEAUMARCHES



Plan de masse projet (zoom)


Echelle : 1:500

Date :04/01/2024


PC
-02.c-

Les présents plans sont exclusivement destinés à l'obtention de l'autorisation administrative. Ils ne sont pas des plans d'exécution et ne peuvent en aucun cas servir à la réalisation de la construction.

Coupe A-A (Nord-Sud)

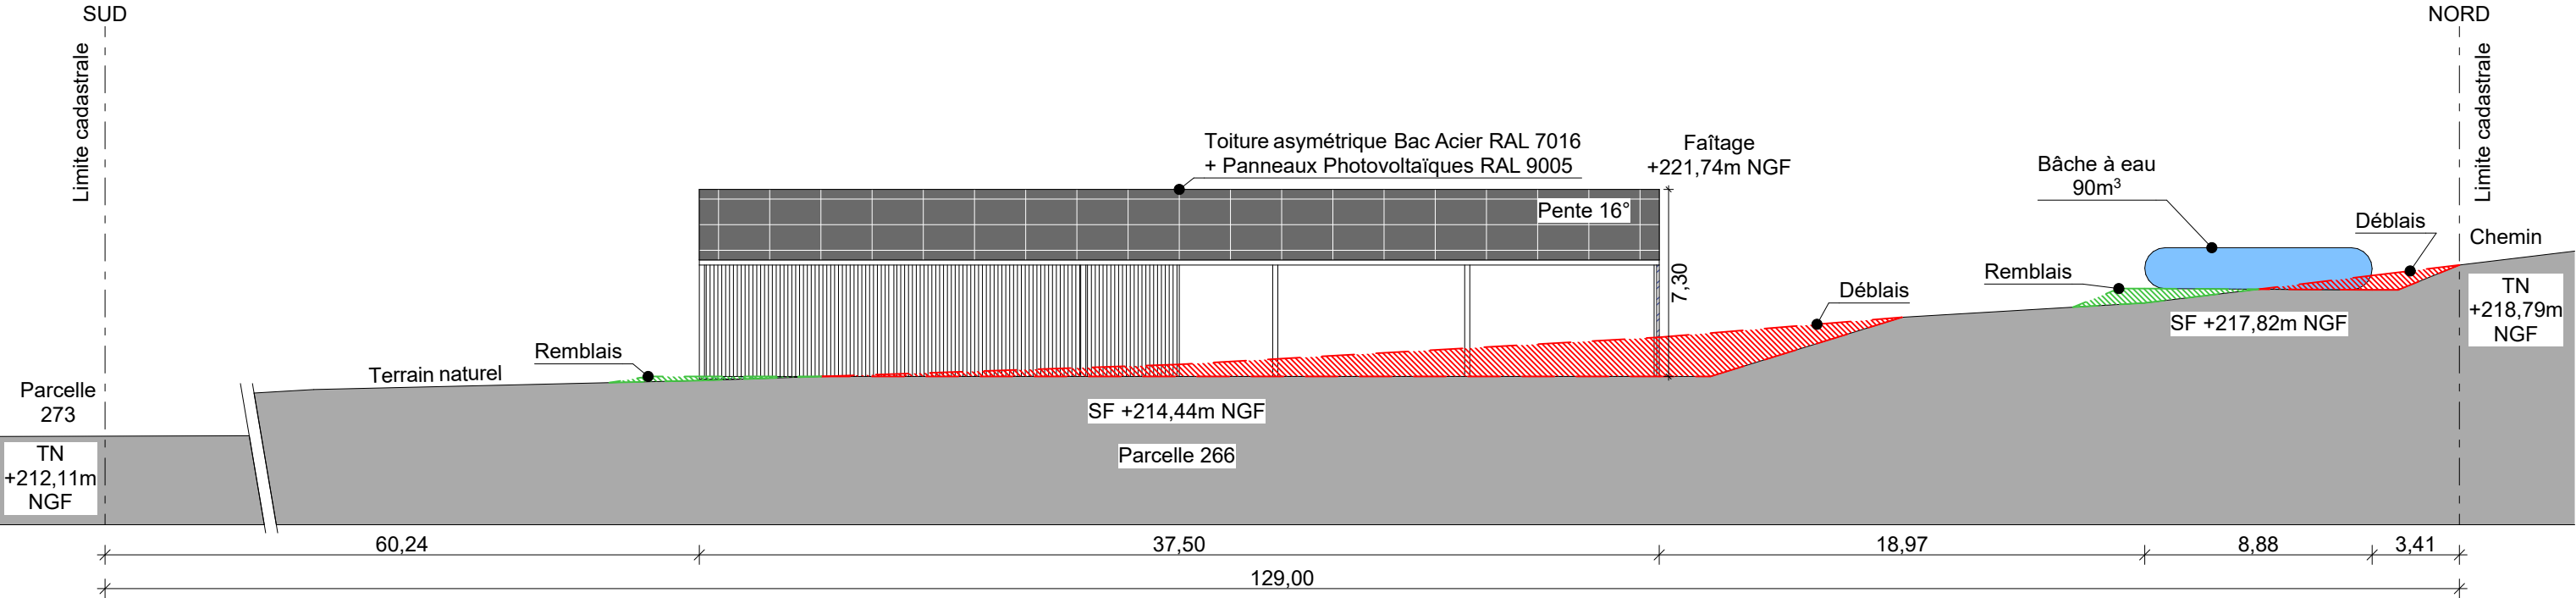

Coupe B-B (Est-Ouest)

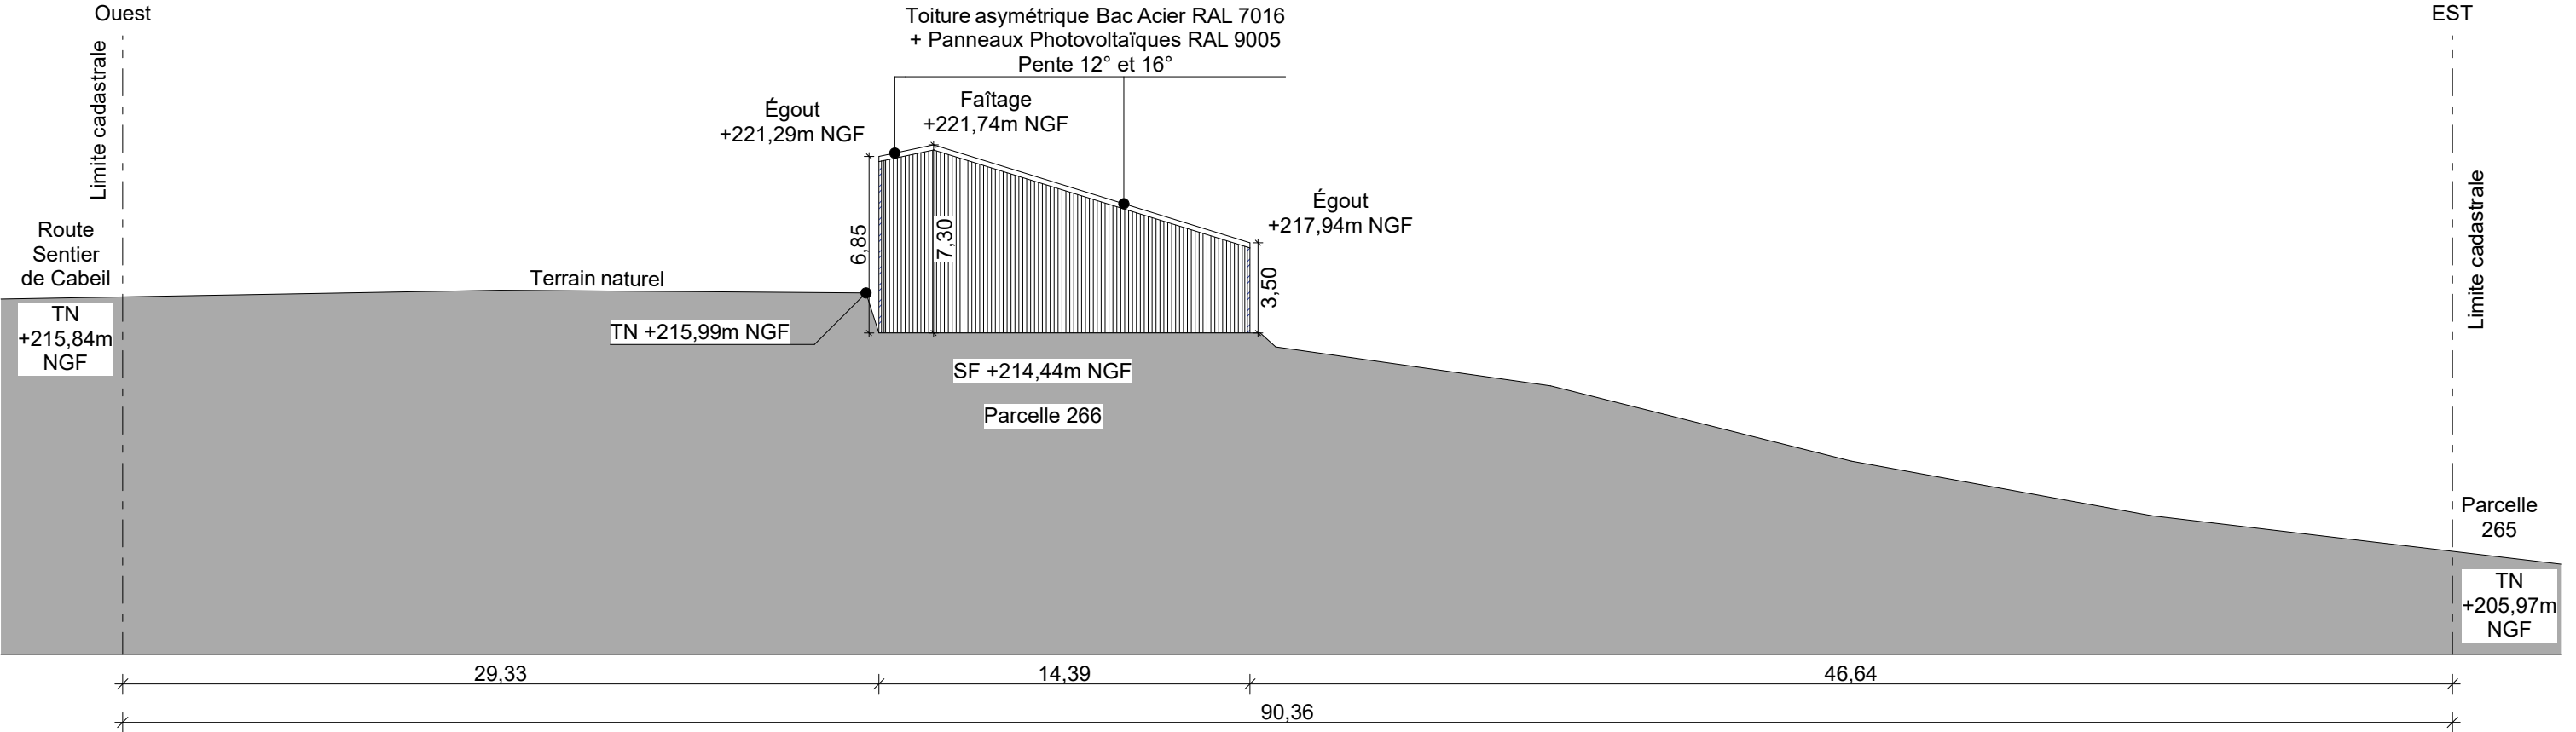

Tresseras Architecture - Siret 882 278 120 00010
Lieu dit " Le Billon " - 33840 CAPTIEUX
07 57 87 99 10 - mathieu@unarchidanslesbo.is

Bâtiment à usage agricole avec toiture photovoltaïque
Lieu-dit Cayron 32160 BEAUMARCHES
EARL SAINT SAUVEUR
Quartier Cayron A Cabeil 32160 BEAUMARCHES



Coupe de terrain
Echelle : 1:250
Date :04/01/2024

PC
-03-

1- OBJET DE LA DEMANDE

La demande de permis de construire porte sur la construction d'un bâtiment de 37,50m par 14,39m à usage agricole avec toiture photovoltaïque. Ce bâtiment servira au stockage de matériel et de fourrage.

2- LE SITE

Le projet se situe au Lieu-dit Cayron 32160 BEAUMARCHES dans le département du Gers. Le terrain concerné par le projet est composé d'une unité foncière n°266, section 000 D d'une surface totale de 14 360m². Le terrain se trouve à une altitude moyenne de 214 m au dessus de la mer. Il s'inscrit dans un paysage à identité rurale. L'accès au projet se fait par la route sentier de Cabeil située à l'Ouest du bâtiment.

3- LE PROJET

Le projet a pour objet la construction d'un bâtiment de forme rectangulaire (longueur 37,50m; largeur 14,39m) en structure métallique, composé de 5 travées de 7,50 mètres d'entraxe. La toiture sera constituée d'une double pente asymétrique (pente de 12° et 16°), avec pour couverture un bac acier (RAL 7016) anti condensation sur les 2 versants. Des panneaux photovoltaïques (RAL 9005) viendront recouvrir le bac acier sur les 2 versants permettant de créer une centrale de production d'électricité photovoltaïque totale de 114 kWc. Ce bâtiment sera couvert et clos sur les façades Nord et Est et la moitié de la façade Ouest par un bardage en bois douglas. Un terrassement sera réalisé pour la mise en oeuvre d'une plateforme en grave compactée. Les eaux pluviales seront collectées par des gouttières et descentes afin d'être infiltrées sur le terrain.

4- RACCORDEMENT AUX RESEAUX

Le bâtiment n'est pas raccordé aux réseaux d'eau, ni d'assainissement, ni d'électricité. Il n'y a donc pas de besoins en alimentation à ces niveaux là.

Seule l'électricité produite par la centrale photovoltaïque est renvoyée dans le réseau ENEDIS via un point de livraison situé en bordure de la parcelle 266 à l'Est du bâtiment (PDL).

L'emplacement du point de livraison indiqué dans les pièces graphiques de l'autorisation d'urbanisme n'apparaît qu'à titre indicatif.

Le positionnement du point de livraison et d'un transformateur (le cas échéant) demeure à l'appréciation finale du gestionnaire de réseau en fonction du site et des équipements déjà existants.

5- SECURITE INCENDIE

Une bache à eau de 90m³ sera à prévoir sur la parcelle 266, au Nord du bâtiment (Cf PC 02 - Plan de masse), Il faudra prévoir une aire d'aspiration de 8x4m, ainsi qu'une aire de retournement en T.

6- VOLET PAYSAGER

Afin d'implanter le bâtiment les arbustes seront déplacés.



Tresseras Architecture - Siret 882 278 120 00010
Lieu dit " Le Billon " - 33840 CAPTIEUX
07 57 87 99 10 - mathieu@unarchidanslesbo.is

Bâtiment à usage agricole avec toiture photovoltaïque

Lieu-dit Cayron 32160 BEAUMARCHES

EARL SAINT SAUVEUR
Quartier Cayron A Cabeil 32160 BEAUMARCHES



Notice d'insertion

Echelle :

Date :04/01/2024


PC
-04-

Les présents plans sont exclusivement destinés à l'obtention de l'autorisation administrative. Ils ne sont pas des plans d'exécution et ne peuvent en aucun cas servir à la réalisation de la construction.




Tresseras Architecture - Siret 882 278 120 00010
Lieu dit " Le Billon " - 33840 CAPTIEUX
07 57 87 99 10 - mathieu@unarchidanslesbo.is


Façade Nord (fermée)

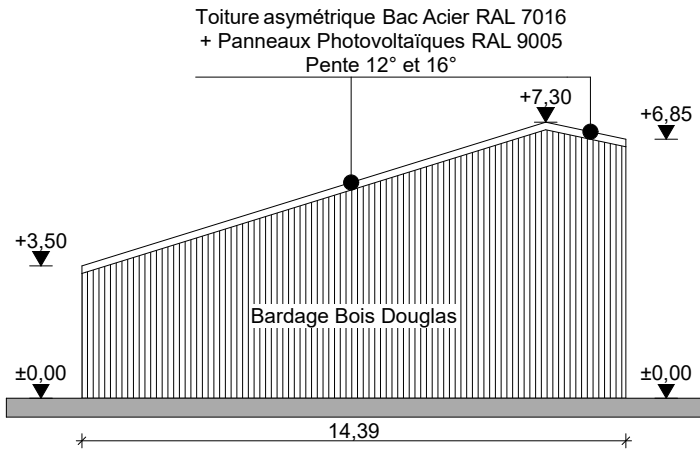


Façade Sud (ouverte)

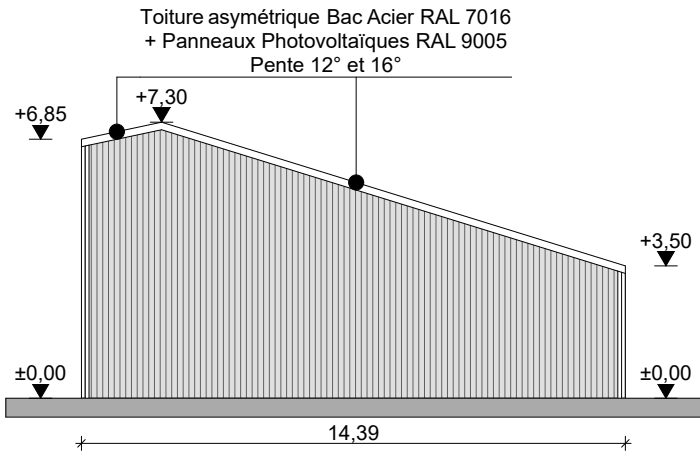

Façade Est (fermée)

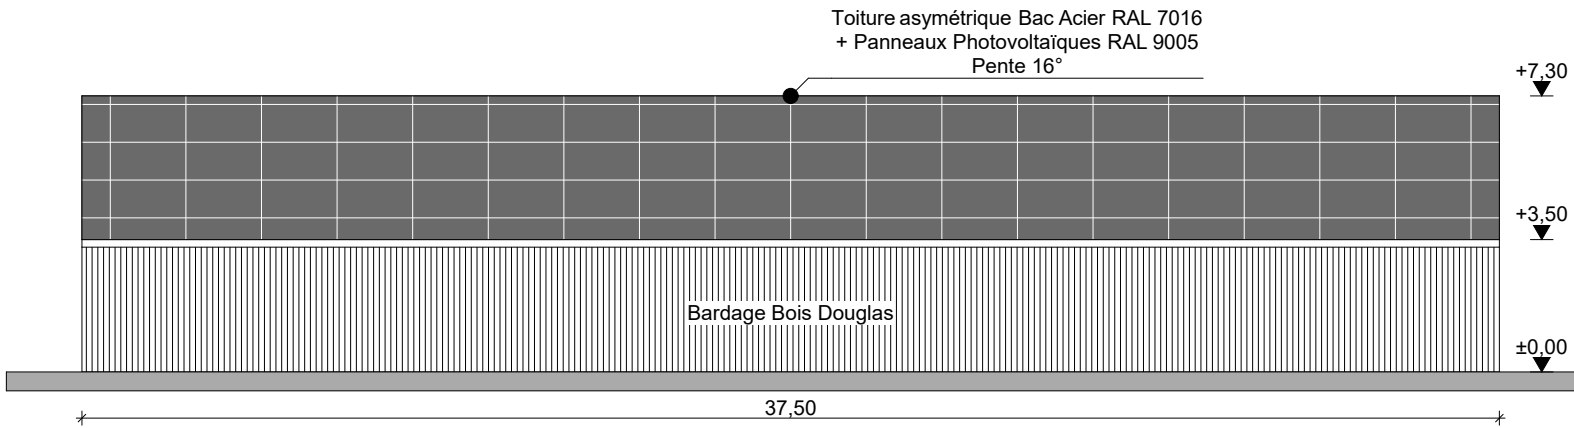

Façade Ouest (semi ouverte)

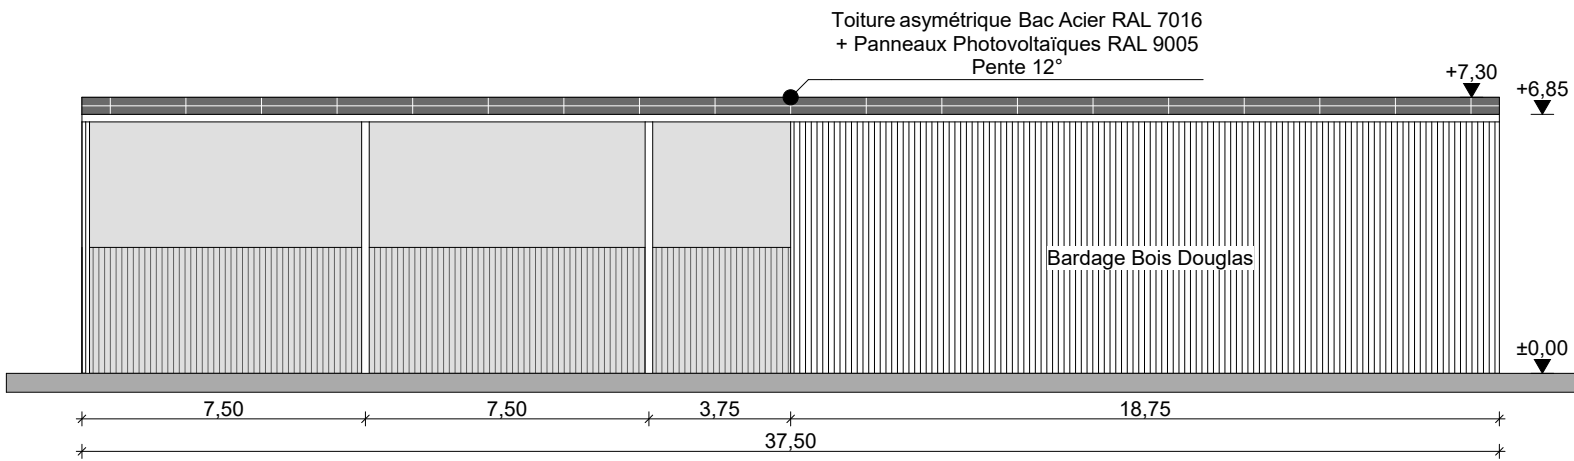

Bâtiment à usage agricole avec toiture photovoltaïque

Lieu-dit Cayron 32160 BEAUMARCHES
EARL SAINT SAUVEUR
Quartier Cayron A Cabeil 32160 BEAUMARCHES




Plan de façades


Echelle : 1:200

Date :04/01/2024

PC
-05.a-

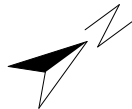

Toiture asymétrique Bac Acier RAL 7016
+ Panneaux Photovoltaïques RAL 9005

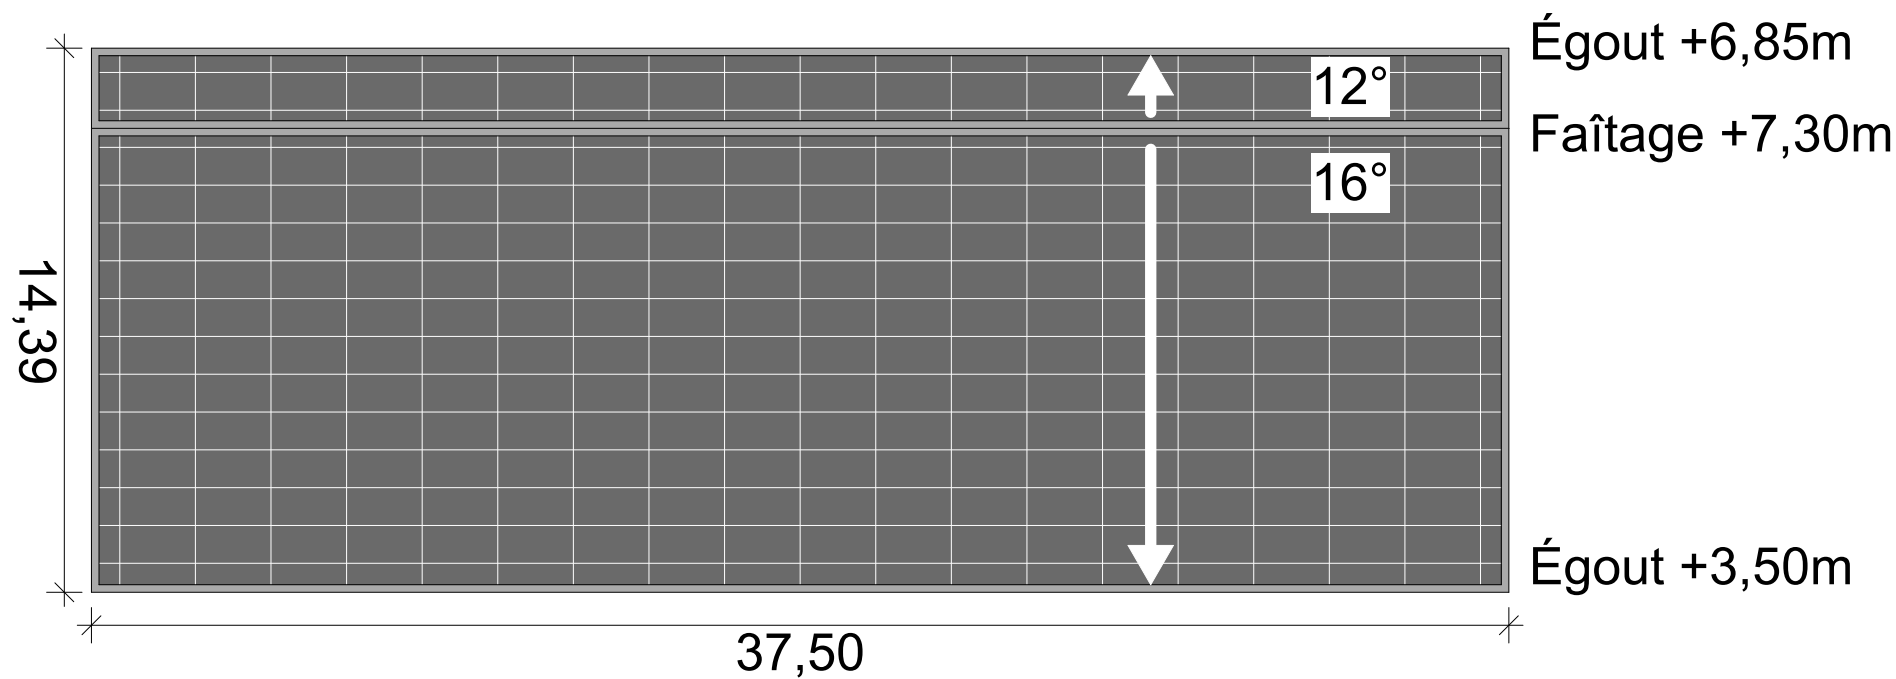

Tresseras Architecture - Siret 882 278 120 00010
Lieu dit " Le Billon " - 33840 CAPTIEUX
07 57 87 99 10 - mathieu@unarchidanslesbo.is

Bâtiment à usage agricole avec toiture photovoltaïque

Lieu-dit Cayron 32160 BEAUMARCHES
EARL SAINT SAUVEUR
Quartier Cayron A Cabeil 32160 BEAUMARCHES



Plan de toiture
Echelle : 1:200
Date :04/01/2024

PC
-05.b-



Photo avant insertion



Photo après insertion



Tresseras Architecture - Siret 882 278 120 00010
Lieu dit " Le Billon " - 33840 CAPTIEUX
07 57 87 99 10 - mathieu@unarchidanslesbo.is

Bâtiment à usage agricole avec toiture photovoltaïque
Lieu-dit Cayron 32160 BEAUMARCHES
EARL SAINT SAUVEUR
Quartier Cayron A Cabeil 32160 BEAUMARCHES



Insertion paysagère
Echelle :
Date :04/01/2024

PC
-06-



Tresseras Architecture - Siret 882 278 120 00010
Lieu dit " Le Billon " - 33840 CAPTIEUX
07 57 87 99 10 - mathieu@unarchidanslesbo.is

Bâtiment à usage agricole avec toiture photovoltaïque

Lieu-dit Cayron 32160 BEAUMARCHES
EARL SAINT SAUVEUR
Quartier Cayron A Cabeil 32160 BEAUMARCHES



Documents photographiques
Echelle : 1:1000
Date :04/01/2024

PC
-07/08-



UN ARCHITECTE DANS LES BOIS

Tresseras Architecture - Siret 882 278 120 00010
Lieu dit " Le Billon " - 33840 CAPTIEUX
07 57 87 99 10 - mathieu@unarchidanslesbo.is

Bâtiment à usage agricole avec toiture photovoltaïque

Lieu-dit Cayron 32160 BEAUMARCHES

EARL SAINT SAUVEUR

Quartier Cayron A Cabeil 32160 BEAUMARCHES



Coordonnées sexagésimales

Echelle : 1:500

Date :04/01/2024

PC
-
ANNEXE